


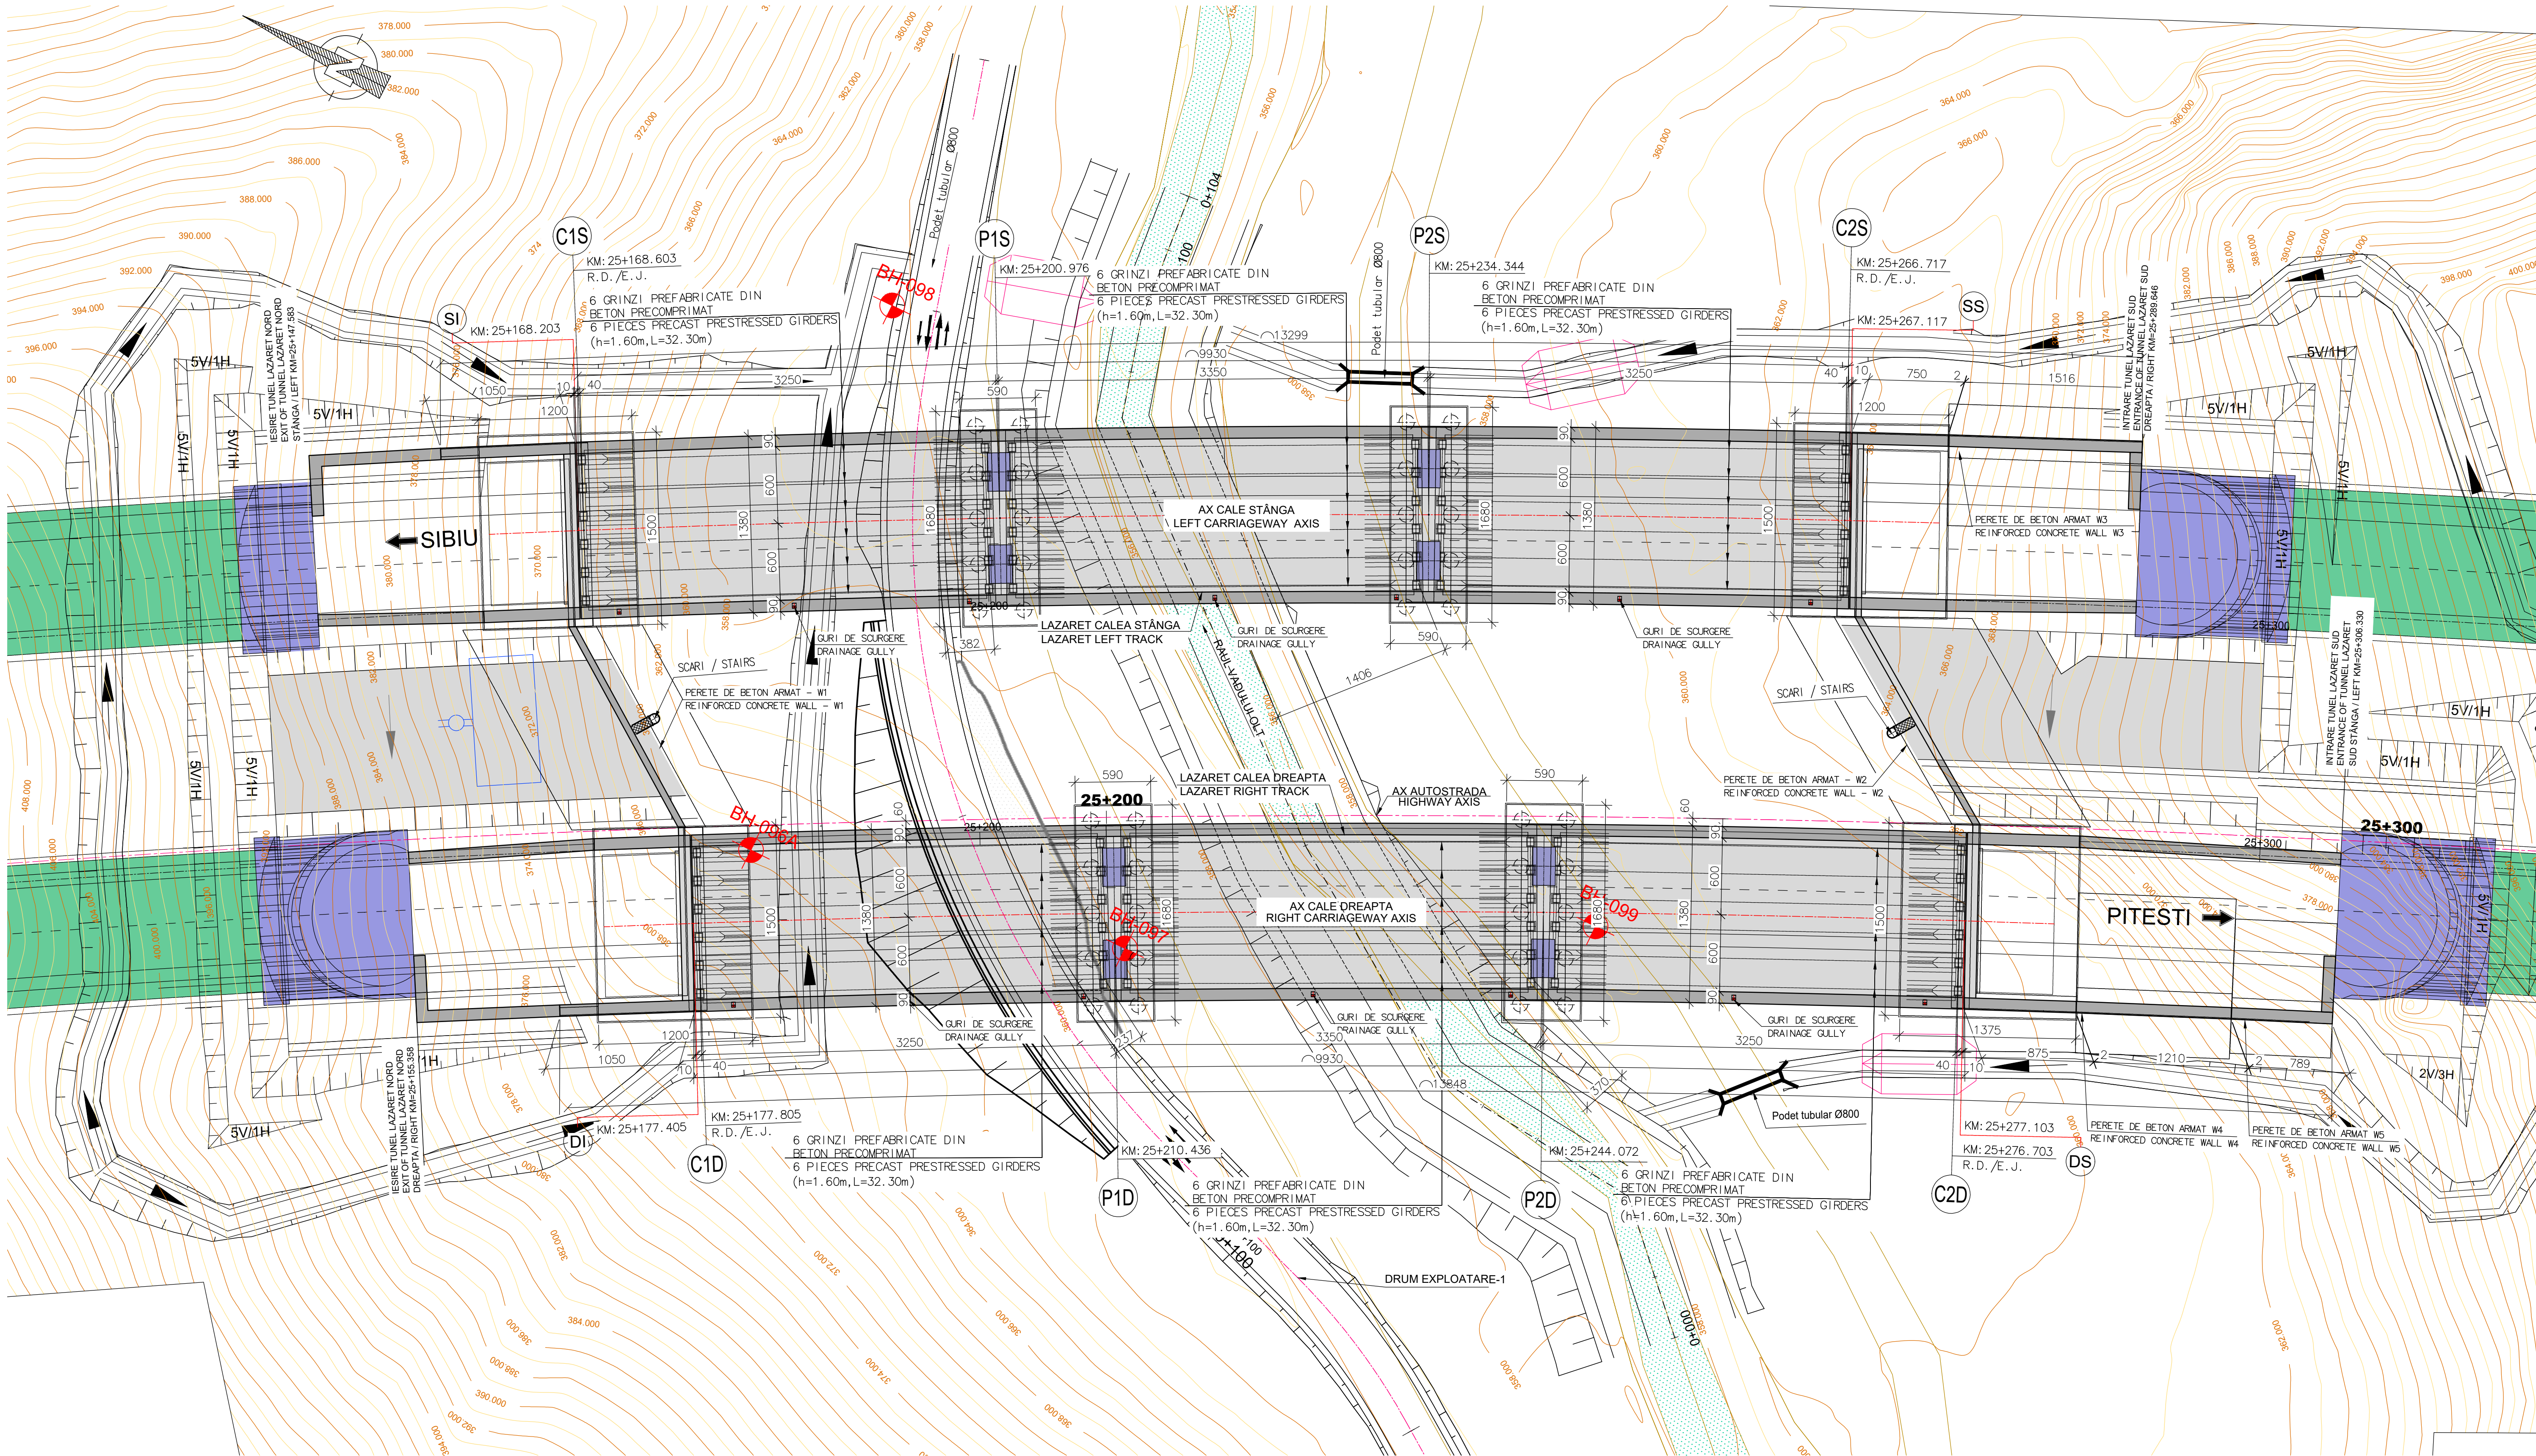

NOTĂ / NOTE :
- TOATE DIMENSIUNILE SUNT DATE IN "cm" DACA NU ESTE SPECIFICAT ALTFEL /
ALL DIMENSIONS ARE IN "cm" UNLESS OTHERWISE SPECIFIED.

ORIGINAL SIZE A1

BENEFICIAR / BENEFICIARY :

PROIECT CO-FINANȚAT DIN FONDUL DE COEZIUNE PRIN
PROGRAMUL OPERATIONAL INFRASTRUCTURA MARE

ANTREPRENOR / CONTRACTOR :

PROIECTANT / DESIGNER :

TITLU PROIECT / NAME OF PROJECT :
Proiectare și Executie Autostrada
Sibiu-Pitești, Secțiunea 2: Boita-Cornetu
FAZA / PHASE :
FAZA - 3 : Proiect Tehnic de Executie (PTE)
PHASE - 3 : Technical Execution Project
NR. CONTRACT :
92/11066/15.02.2022

SPECIFICATIE
POSITION
NUME
NAME
SEMNAȚURA
SIGNATURE
Sef Echipa Proiectare
Design Manager
Proiectat
Design
Aprobat de
Approved by
Verificator Intern
Internal Checker
Ing. Battal YILDIZ
Ing. Emre ŞENTÜRK
Ing. Burak KURTMAN
Ing. M.Kaan BAŞÇUHADAR

REVISI / REVISIONS
2 06.2026
1 04.2026
0 02.2026
Revisia 2 / Revision 2
Adresa Nr. IRD-RO-ROM007 / OUT / 1325 / MC din data de 15.05.2026,
Adresa Nr. IRD-RO-ROM007 / OUT / 1330 / MC din data de 20.05.2026,
Adresa Nr. IRD-RO-ROM007 / OUT / 1351 / MC din data de 28.05.2026.
Revisia 1 / Revision 1
Adresa Nr. IRD-RO-ROM007 / OUT / 1103 / MC din data de 27.02.2026,
Adresa Nr. IRD-RO-ROM007 / OUT / 1103 / MC din data de 13.03.2026,
Adresa CNAR Nr. 92/22620 din data de 16.03.2026 și CNAR Nr. 92/2204 din data de 19.03.2026.
Prima Editie / First Issue

DATA / DATE :
06.2026
SCALA / SCALE :
1/250
Proiect Tehnic de Executie (PTE)
POD PESTE RAUL VADULUI, DC (STÂNGA / Left) (Km : 25+181 - 25+271)
POD PESTE RAUL VADULUI, DC (Dreapta / Right) (Km : 25+181 - 25+271)
VIA-23 (STÂNGA / Left) (Km : 25+168.203 - 25+267.117)
VIA-23 (Dreapta / Right) (Km : 25+177.405 - 25+277.103)
DISPOZIȚIE GENERALA - VEDERE PLANA / GENERAL LAYOUT
Descrierea Proiectului / Project Name
Faza / Phase
Origine / Origin
Activitate / Activity
Locul de Lucru / Work Place
Tip / Type
Sector / Sector
Numar / Number
Index / Index
SP23YPPSTVIA23PV4001A02