

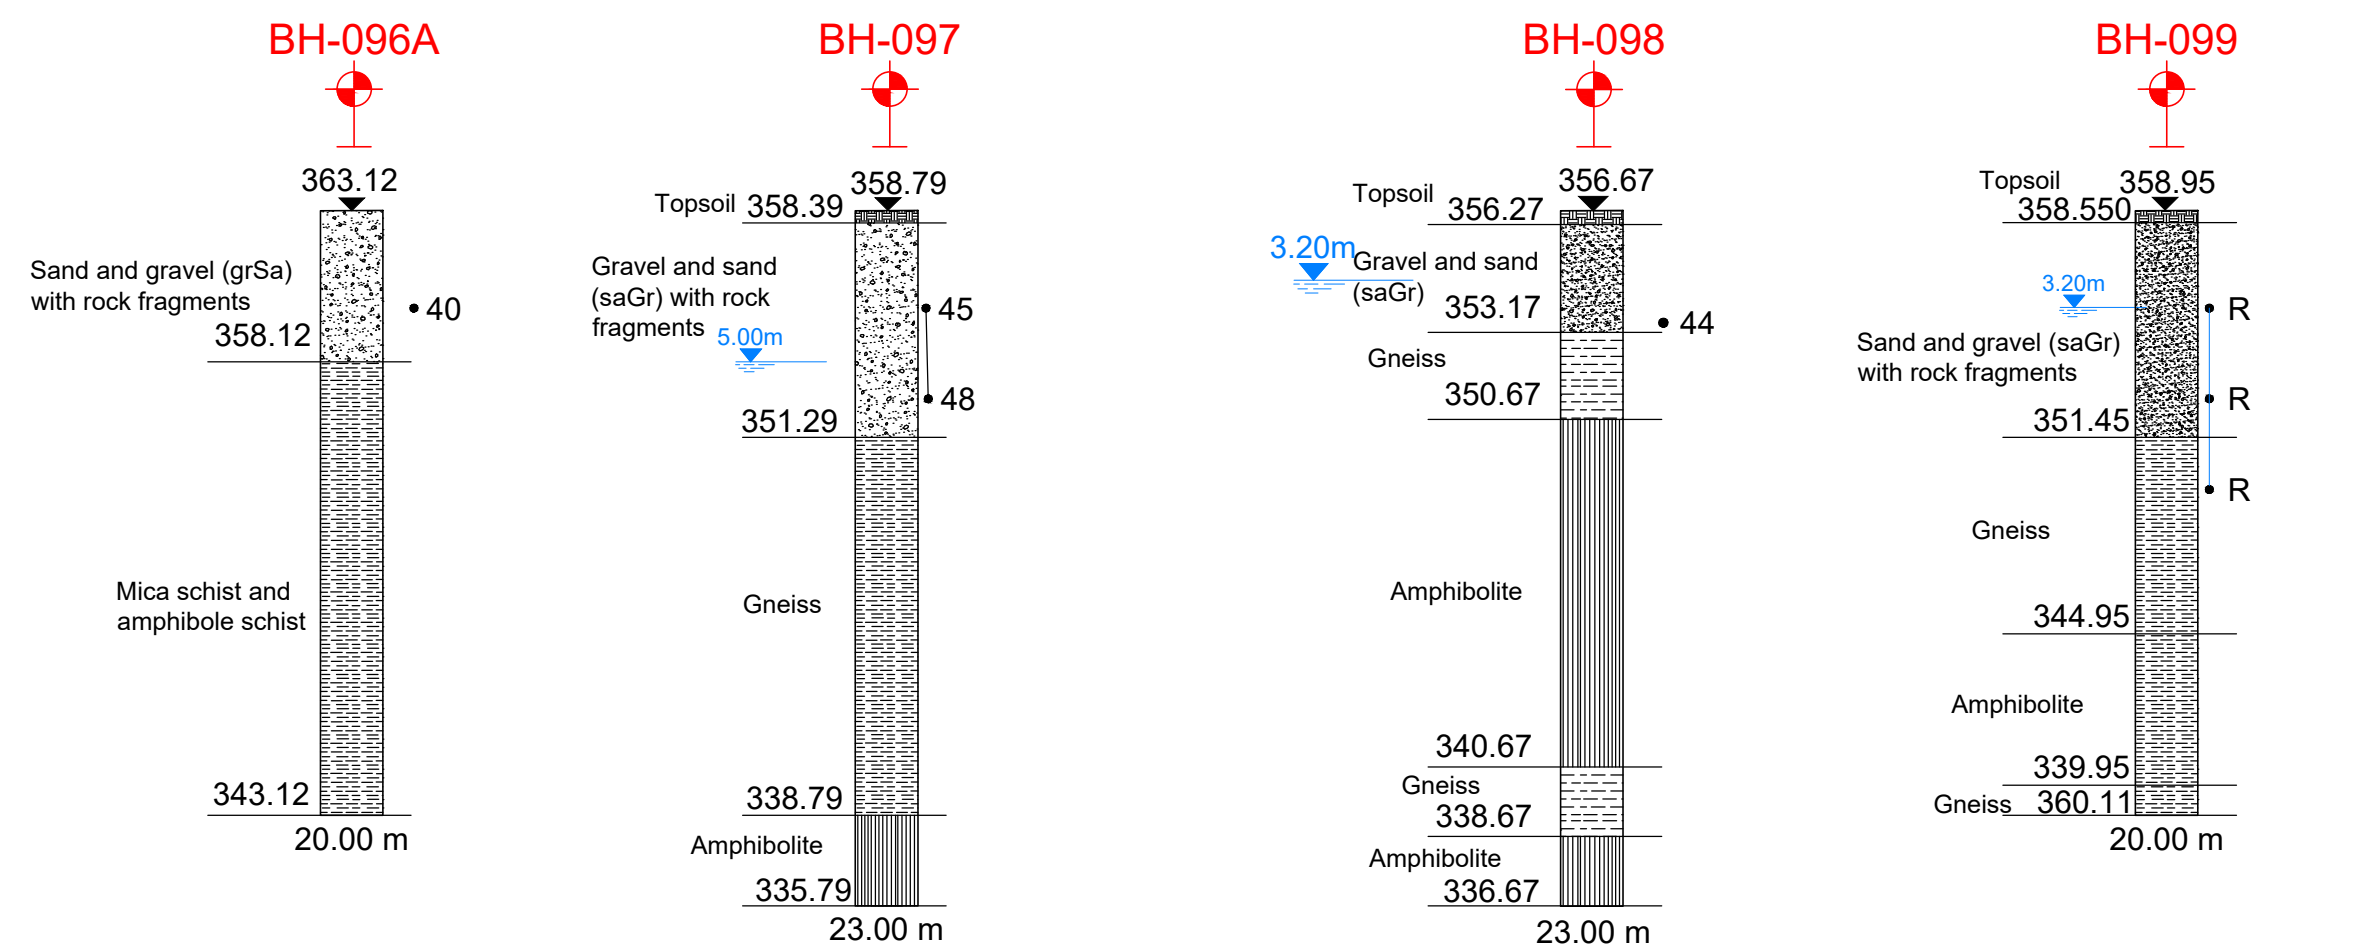


ELEVATIE STÂNGA / LEFT SIDE ELEVATION 1:250


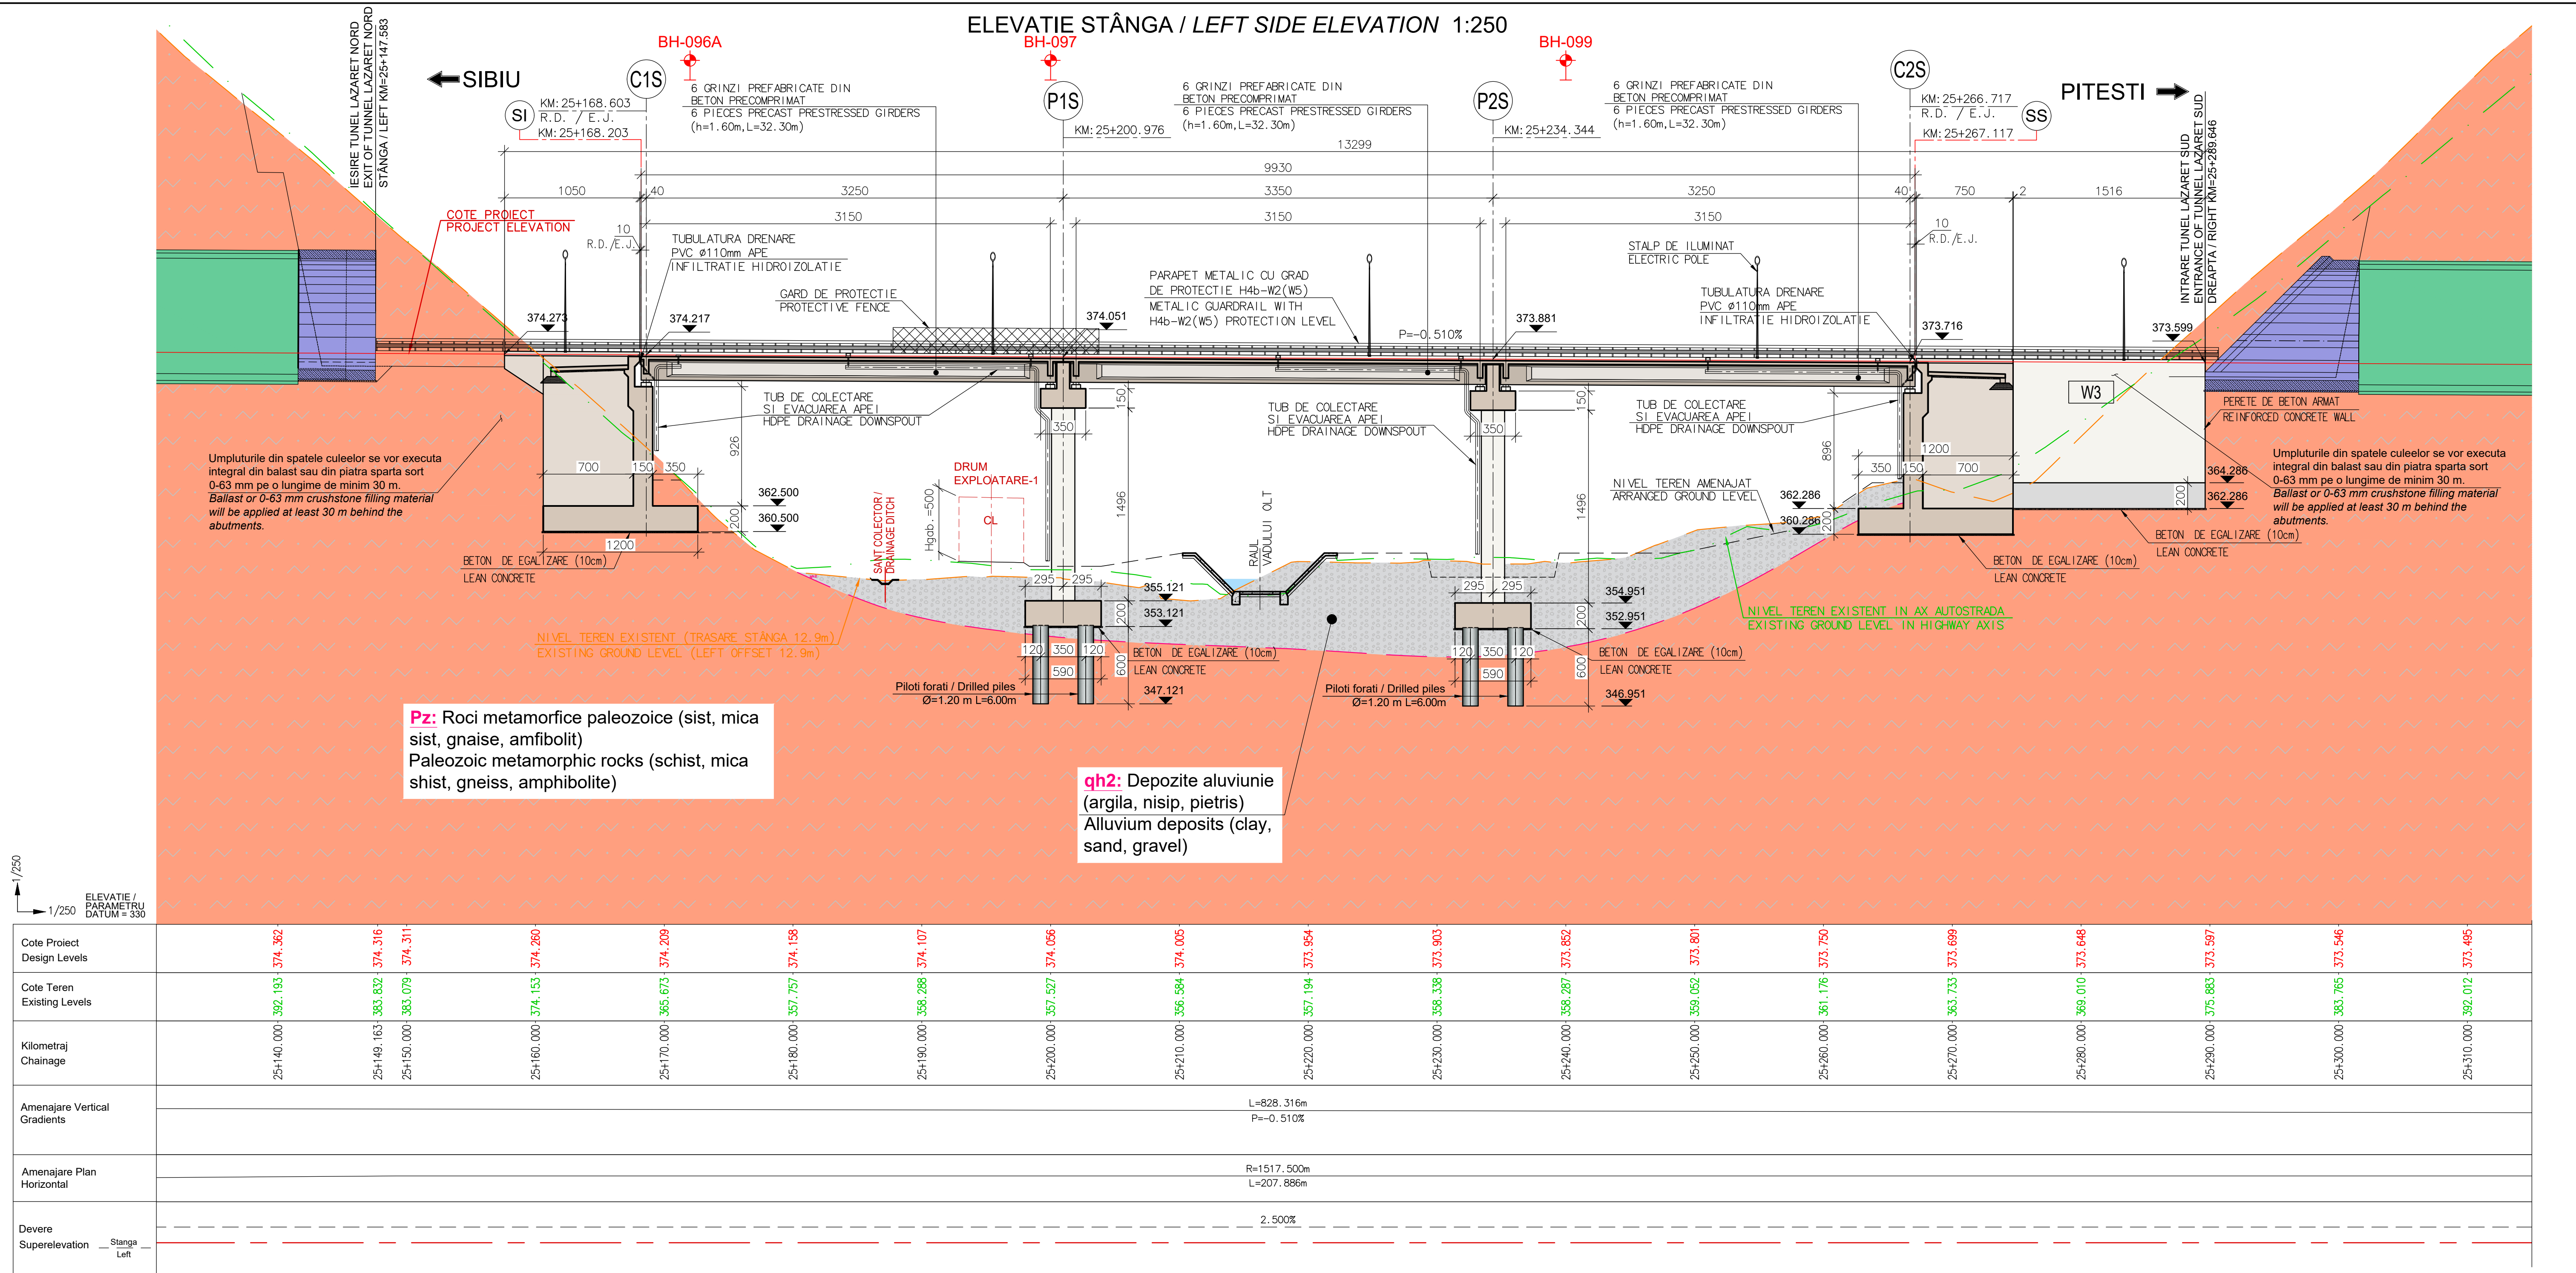


DESCRIERE / DESCRIPTIONS :

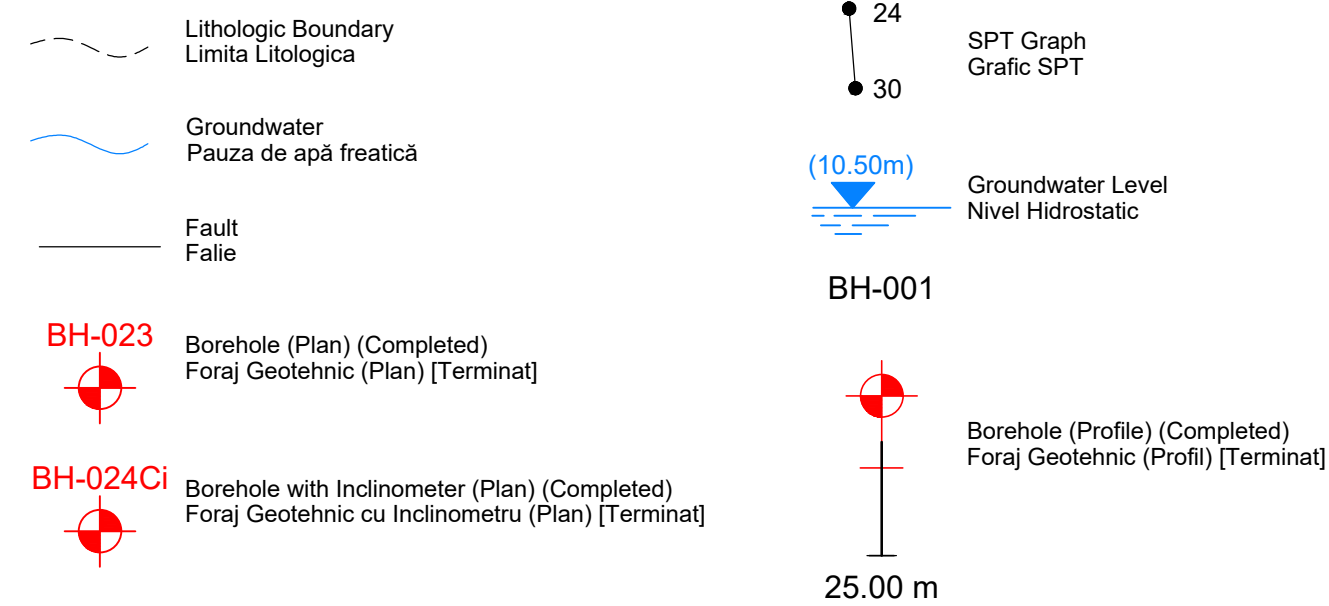


NOTĂ / NOTE :
- TOATE DIMENSIUNILE SUNT DATE IN "cm" DACA NU ESTE SPECIFICAT ALTTEL /
ALL DIMENSIONS ARE IN "cm" UNLESS OTHERWISE SPECIFIED.

BENEFICIAR / BENEFICIARY :		ANTREPRENOR / CONTRACTOR :		PROIECTANT / DESIGNER :		TITLU PROIECT / NAME OF PROJECT :		SPECIFICATIE POSITION		NUME NAME		SEMNATURA SIGNATURE		DATA / DATE :		Proiect Tehnic de Executie (PTE)	
						Proiectare și Executie Autostrada Sibiu-Pitești, Secțiunea 2: Boita-Cornetu		Sef Echipa Proiectare Design Manager		Ing. Battal YILDIZ				06.2026		POD PESTE RAUL VADULUI, DC (STÂNGA / Left) (Km : 25+181 - 25+271) POD PESTE RAUL VADULUI, DC (Dreapta / Right) (Km : 25+181 - 25+271) VIA-23 (STÂNGA / Left) (Km : 25+168.203 - 25+267.117) VIA-23 (Dreapta / Right) (Km : 25+177.405 - 25+277.103) PROFIL LONGITUDINAL / LONGITUDINAL PROFILE 1/2	
PROIECT CO-FINANȚAT DIN FONDUL DE COEZIUNE PRIN PROGRAMUL OPERATIONAL INFRASTRUCTURA MARE						FAZA - 3 : : Proiect Tehnic de Executie (PTE) PHASE - 3 : Technical Execution Project		NR. CONTRACT :		Ing. Burak KURTMAN				04.2026			
								Verificator Intern Internal Checker		Ing. M.Kaan BAŞÇUHADAR				02.2026			
														PRIMA EDITIE / FIRST ISSUE			
														DESCRIERE / DESCRIPTION		SP23YPPSTVIA23LP4001A02	

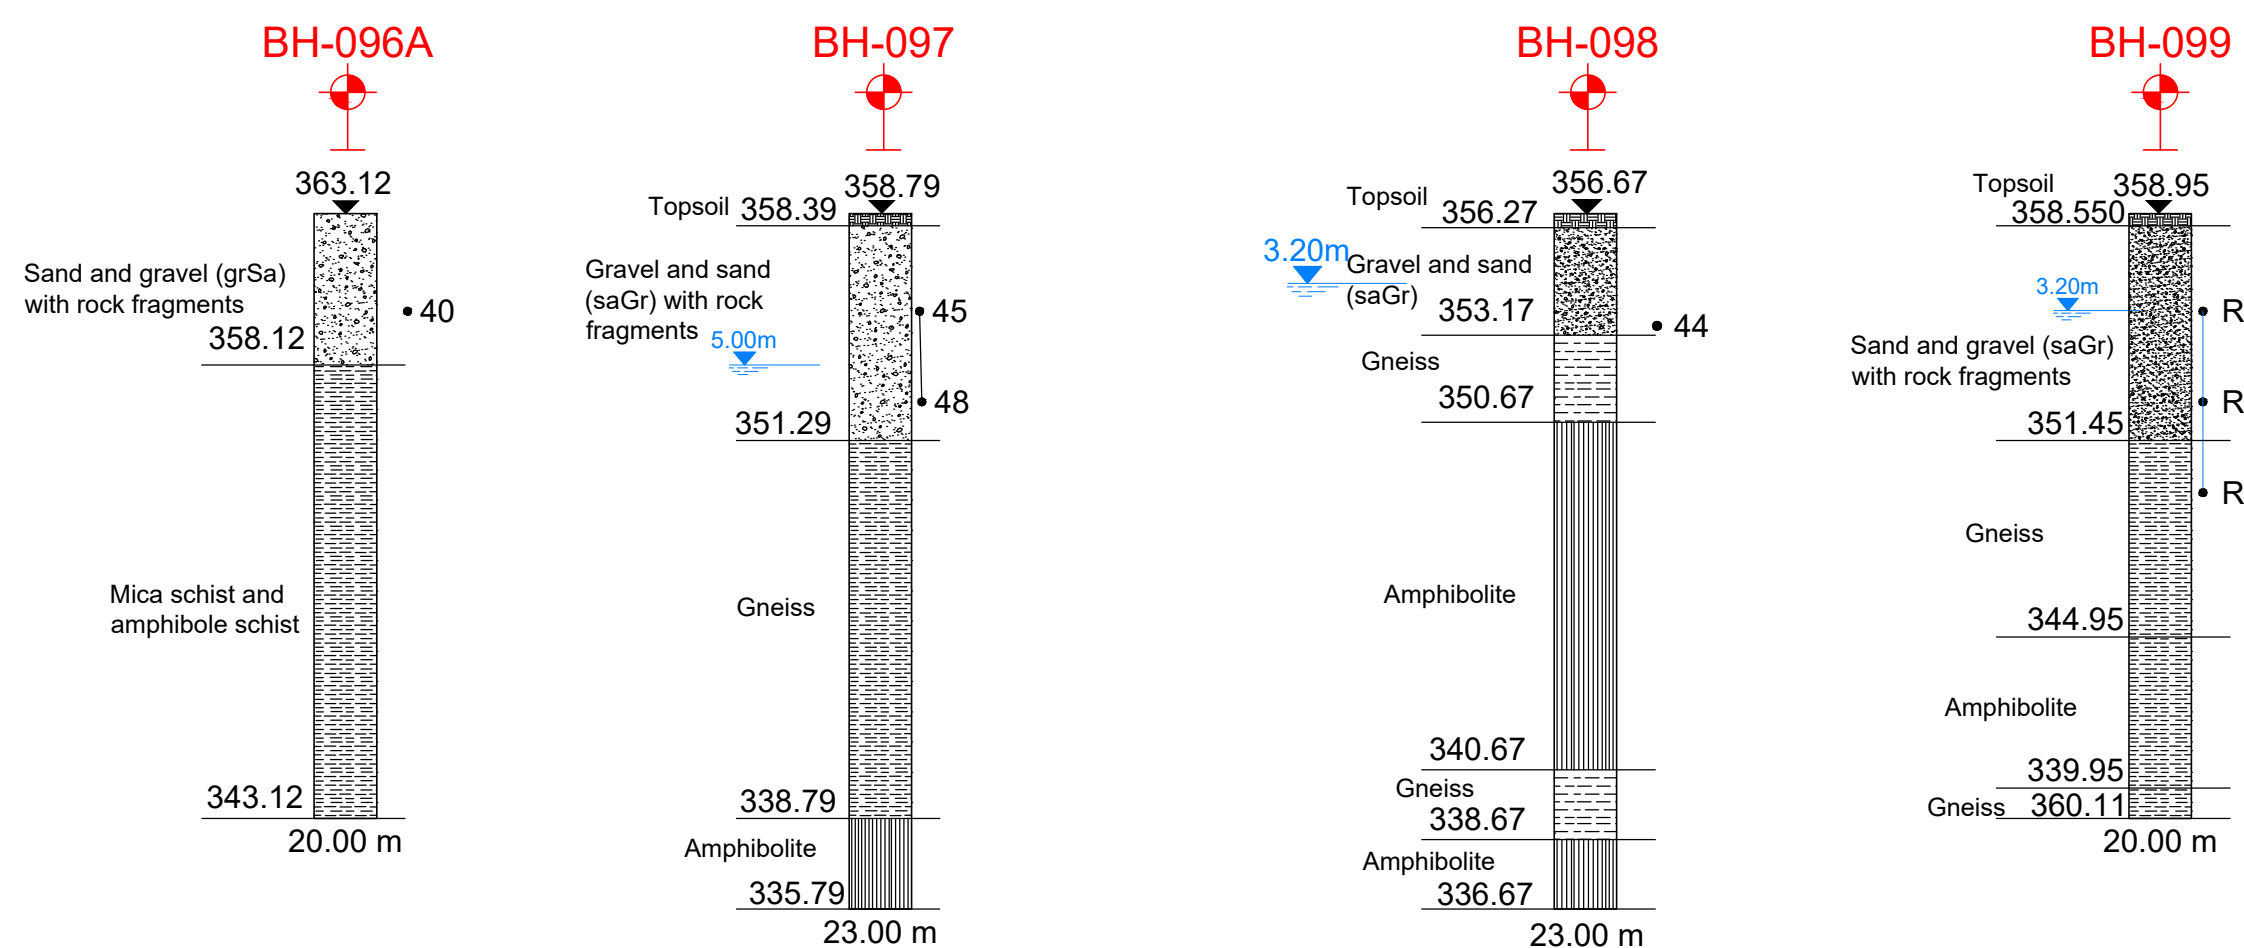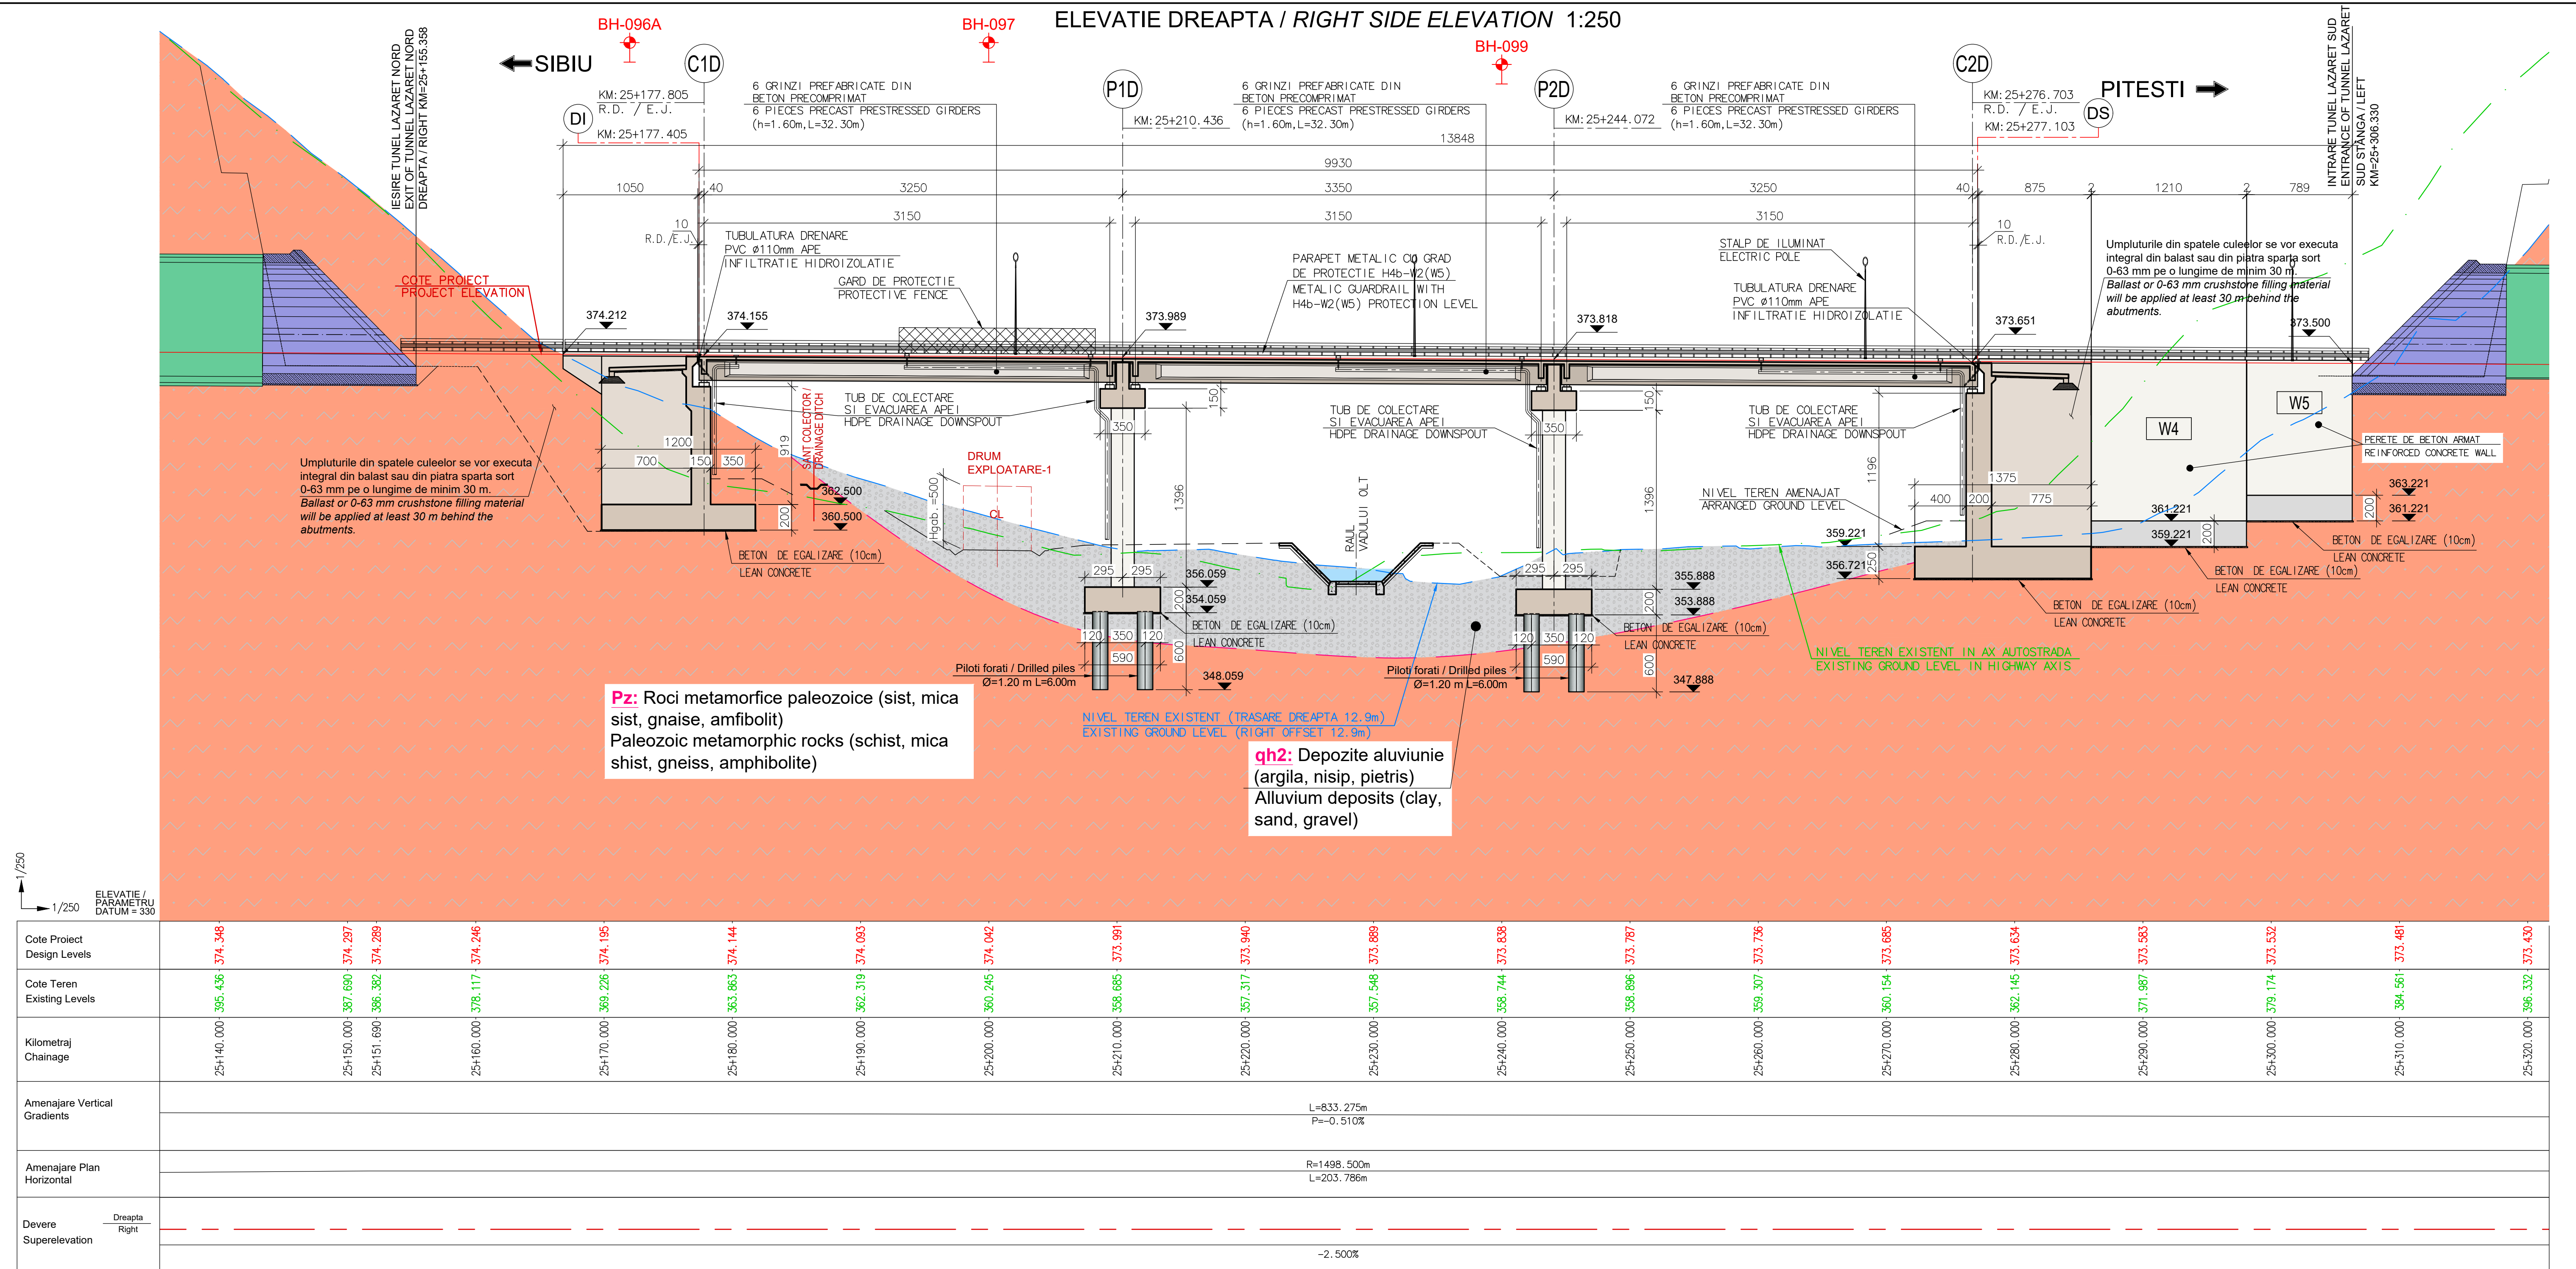

DESCRIERE / DESCRIPTIONS :

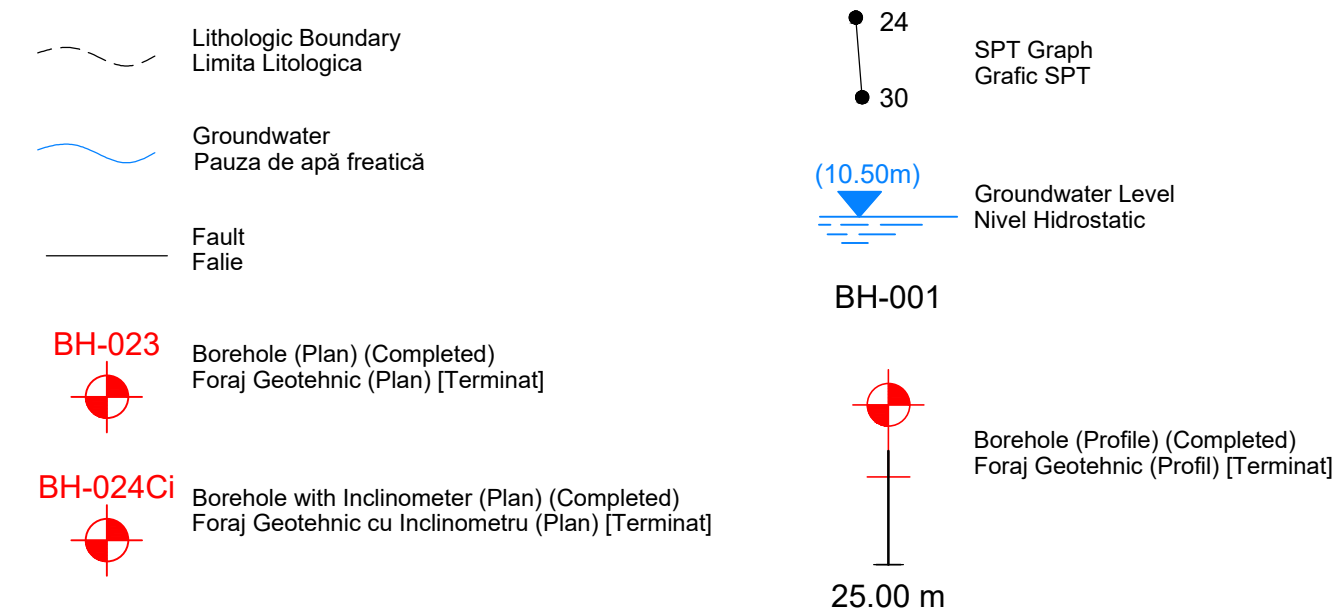

NOTĂ / NOTE :
- TOATE DIMENSIUNILE SUNT DATE IN "cm" DACA NU ESTE SPECIFICAT ALTTEL / ALL DIMENSIONS ARE IN "cm" UNLESS OTHERWISE SPECIFIED.

BENEFICIAR / BENEFICIARY :		ANTREPRENOR / CONTRACTOR :		PROIECTANT / DESIGNER :		TITLU PROIECT / NAME OF PROJECT :		SPECIFICATIE POSITION		NUME NAME		SEMNAȚURA SIGNATURE		REVISIONS		DATA / DATE :		Proiect Tehnic de Executie (PTE)	
						Proiectare și Executie Autostrada Sibiu-Pitești, Secțiunea 2: Boita-Cornetu		Sef Echipa Proiectare / Design Manager		Ing. Battal YILDIZ				2		06.2026		POD PESTE RAUL VADULUI, DC (STÂNGA / Left) (Km : 25+181 - 25+271)	
PROIECT CO-FINANȚAT DIN FONDUL DE COEZIUNE PRIN PROGRAMUL OPERATIONAL INFRASTRUCTURA MARE						FAZA / PHASE :		Proiectat / Design		Ing. Emre ŞENTÜRK				1		04.2026		VIA-23 (STÂNGA / Left) (Km : 25+168.203 - 25+267.117)	
						NR. CONTRACT :		Aprobat de / Approved by		Ing. Burak KURTMAN				0		02.2026		VIA-23 (Dreapta / Right) (Km : 25+177.405 - 25+277.103)	
						FAZA - 3 : Proiect Tehnic de Executie (PTE)		Verificator Intern / Internal Checker		Ing. M.Kaan BAŞÇUHADAR				NR. DATA		Prima Editie / First Issue		PROFIL LONGITUDINAL / LONGITUDINAL PROFILE 2/2	
																		SP23YPPSTVIA23LP4002A02	