




SECȚIUNE TRANSVERSALA CURENȚA PRIN SUPRASTRUCTURĂ / TYPICAL CROSS SECTION OF SUPERSTRUCTURE 1:50

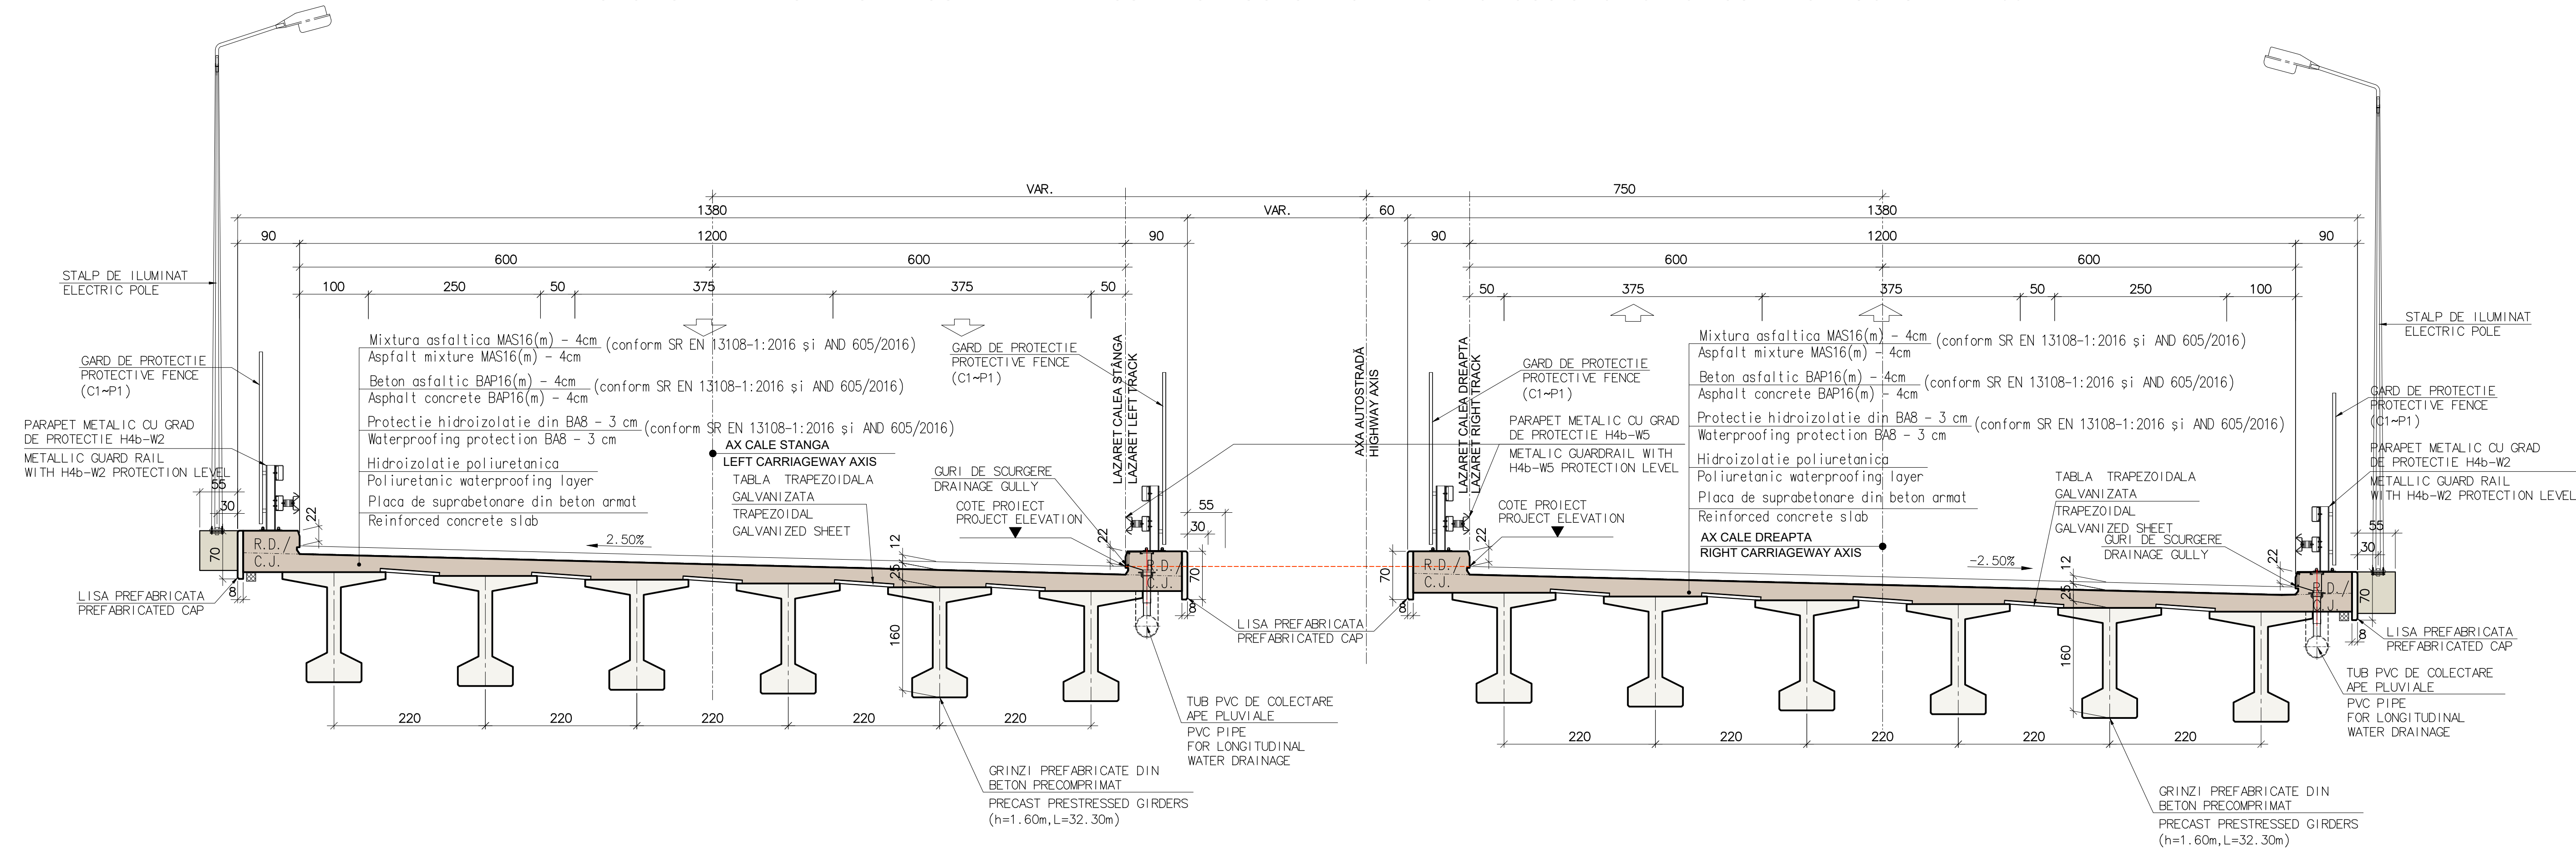

SECȚIUNE ELEVATIE / COLUMN SECTION 1:50

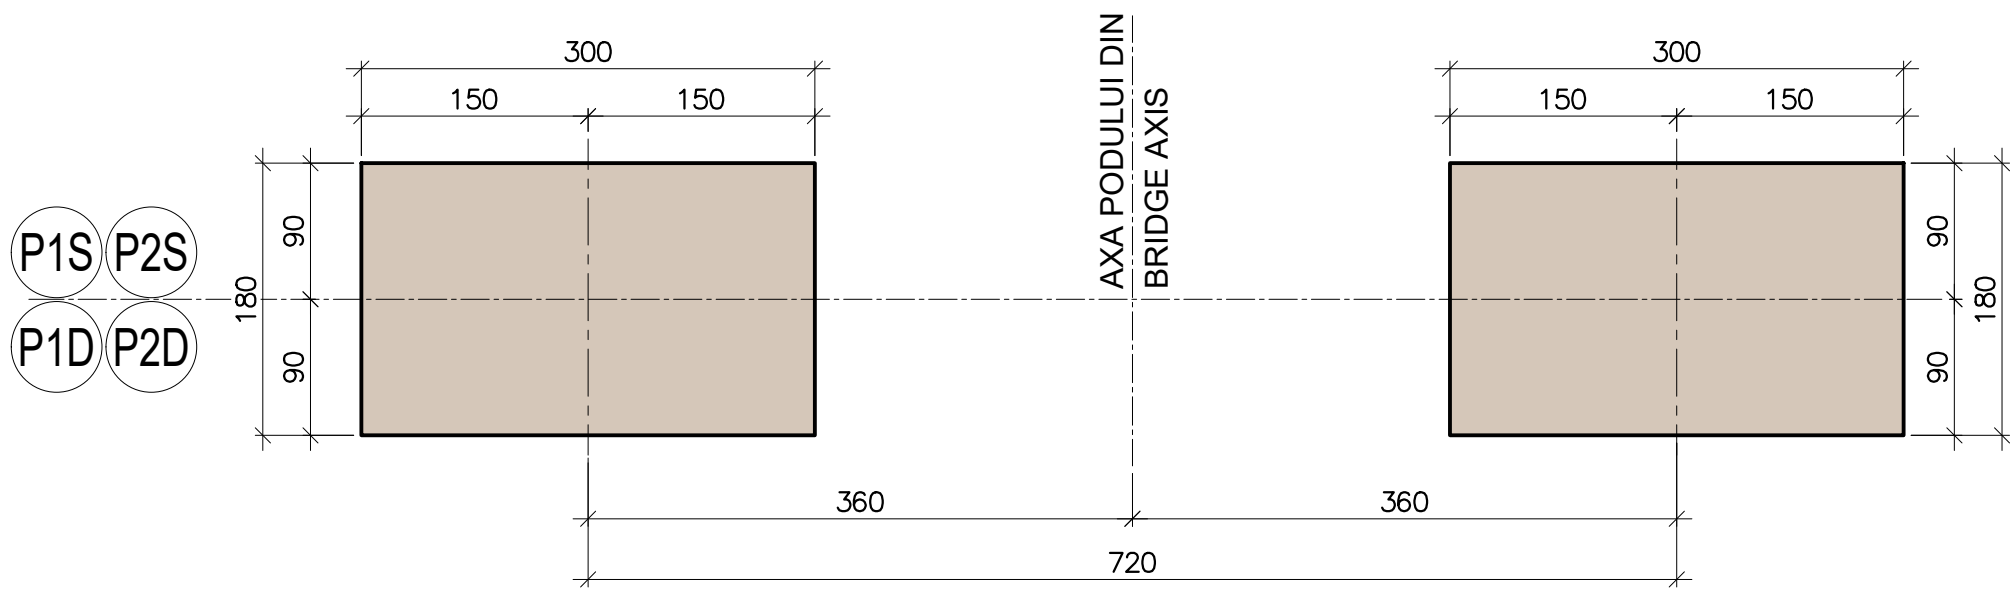

SECȚIUNE GRINDĂ / BEAM SECTION 1:25

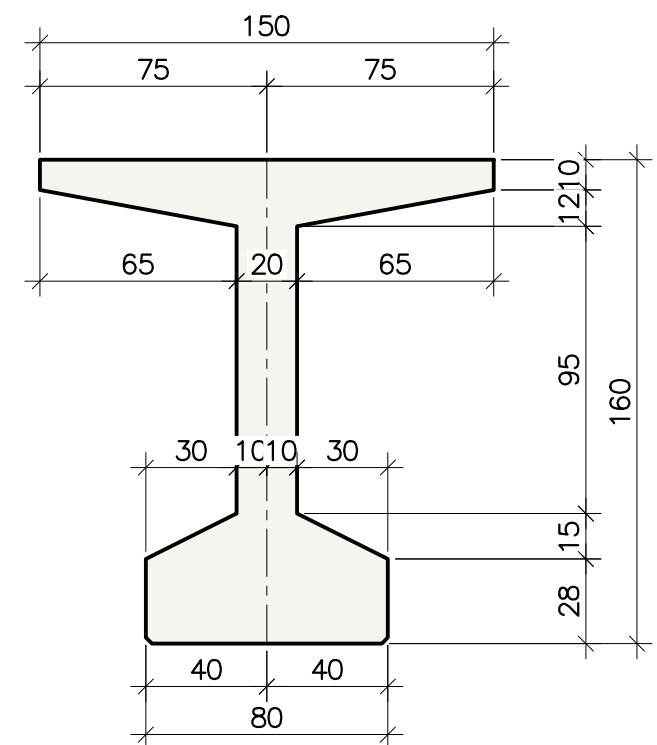


NOTĂ / NOTE :
- TOATE DIMENSIUNILE SUNT DATE IN "cm" DACA NU ESTE SPECIFICAT ALTTEL /
ALL DIMENSIONS ARE IN "cm" UNLESS OTHERWISE SPECIFIED.

ORIGINAL SIZE A1

BENEFICIAR / BENEFICIARY :		ANTREPRENOR / CONTRACTOR :		PROIECTANT / DESIGNER :		TITLUL PROIECT / NAME OF PROJECT :		SPECIFICAȚIE / POSITION		NUME / NAME		SEMNAȚURĂ / SIGNATURE		DATA / DATE : 06.2026		Proiect Tehnic de Execuție (PTE)	
						Proiectare și Execuție Autostrada Sibiu-Pitești, Secțiunea 2: Boita-Cornetu		Sef Echipă Proiectare / Design Manager		Ing. Battal YILDIZ				2 06.2026		Revizia 2 / Revision 2	
PROIECT CO-FINANȚAT DIN FONDUL DE COEZIUNE PRIN PROGRAMUL OPERATIONAL INFRASTRUCTURA MARE						FAZA / PHASE : FAZA - 3 : Proiect Tehnic de Execuție (PTE) PHASE - 3 : Technical Execution Project		Proiectat / Design		Ing. Emre ŞENTÜRK				1 04.2026		Revizia 1 / Revision 1	
						NR. CONTRACT : 92/11066/15.02.2022		Aprobat de / Approved by		Ing. Burak KURTMAN				0 02.2026		Adresa Nr. IRD-RO-ROM007 / OUT / 1181 / MC din data de 13.03.2026.	
								Verificator Intern / Internal Checker		Ing. M.Kaan BAŞÇUHADAR				NR. DATA		Prima Editie / First Issue	
																DESCRIERE / DESCRIPTION	
																SP23YPPSTVIA23TC4001A02	


SECTIUNE TRANSVERSALA CU VEDERE CULEE C1S & C1D /
CROSS SECTION WITH ABUTMENT C1S & C1D VIEW 1:100

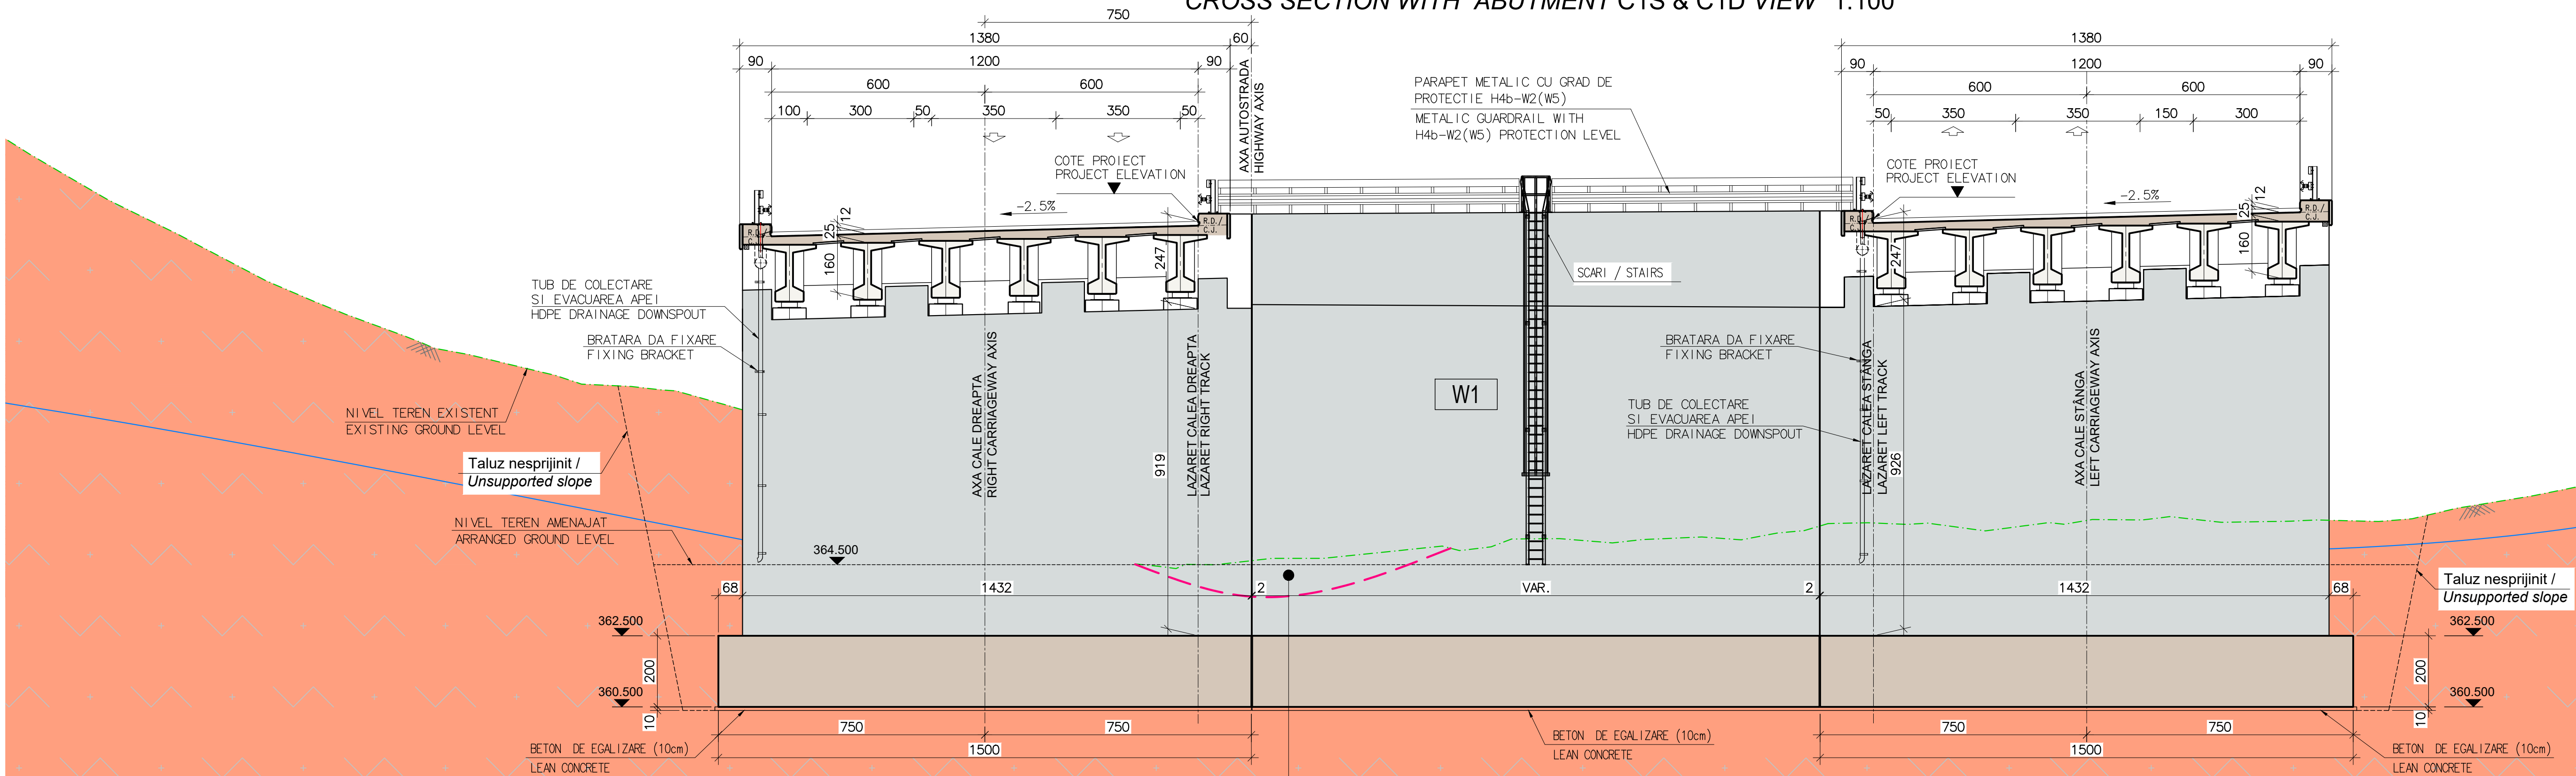

qh2: Depozite aluviunice (argila, nisip, pietris)
Alluvium deposits (clay, sand, gravel)

Pz: Roci metamorfice paleozoice (sist, mica sist, gnaise, amfibolit)
Paleozoic metamorphic rocks (schist, mica schist, gneiss, amphibolite)

SECTIUNE W1 PERETE DE BETON ARMAT 1:100
SECTION ON REINFORCED CONCRETE WALL W1

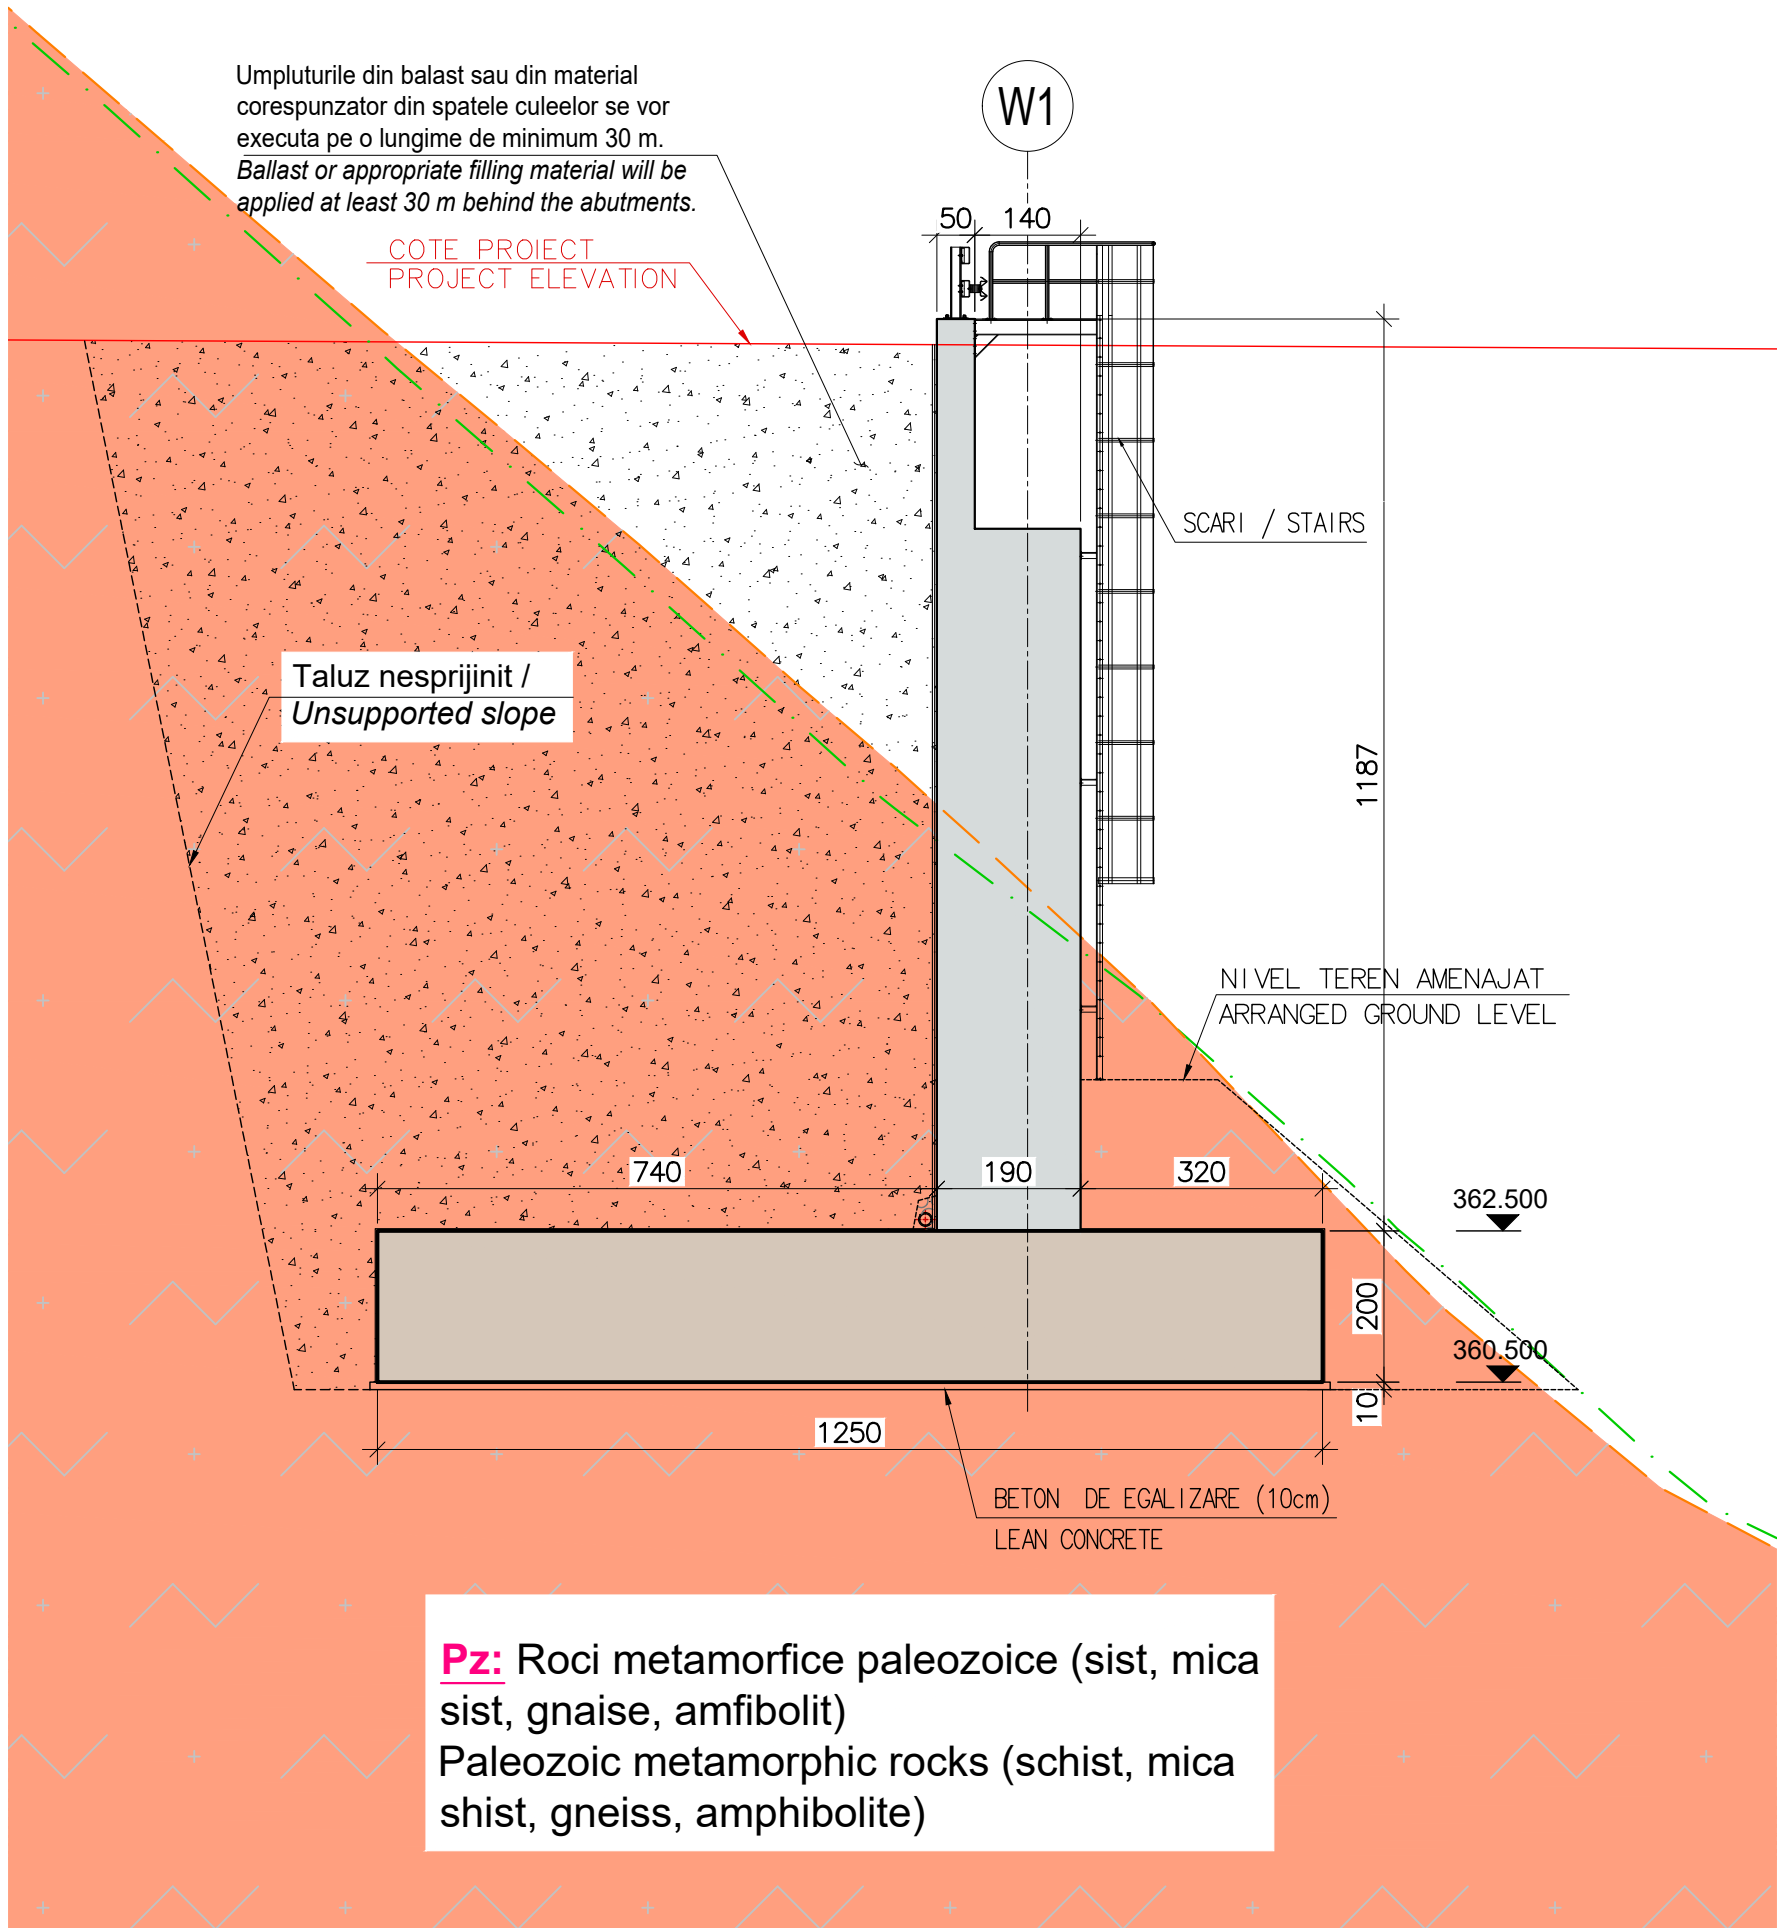

Pz: Roci metamorfice paleozoice (sist, mica sist, gnaise, amfibolit)
Paleozoic metamorphic rocks (schist, mica schist, gneiss, amphibolite)

- Datorita existentei planurilor de sistozitate in masa de roca in zona fundatiilor, dupa excavarea fundatiilor trebuie efectuate verificari cinematice pentru a preveni cedarea datorita discontinuitatilor rocilor.
 - Dupa excavarea fundatiilor, in cazul in care local se intalnesc formatiuni de pamanturi (depozite aluvionare), acestea se vor inlocui cu beton simplu
1. Because of existence of heavily tectonized schistosity planes in the foundation rock mass, after foundation excaavation, kinematical checks must be performed to prevent possible discontinuity controlled failure.
2. After foundation excavation if any soil material is encountered locally it will be replaced by plain concrete.


Pentru sprijinirea debleului necesar constructia podului, va rugam sa consultati raportul „Lucrari de consolidare – Sector 4 -Breviar de calcul. Km 19+150-44+500, Capitolul 2.3.6 Tabelul 7”.

To support the excavation required for the construction of the bridge, please consult the report “Consolidation Works - Sector 4 - Calculation Brief. Km 19+150-44+500, Chapter 2.3.6 Table 7”.


NOTĂ / NOTE :
- TOATE DIMENSIUNILE SUNT DATE IN "cm" DACA NU ESTE SPECIFICAT ALTFEL /
ALL DIMENSIONS ARE IN "cm" UNLESS OTHERWISE SPECIFIED.

BENEFICIAR / BENEFICIARY :		ANTREPRENOR / CONTRACTOR :		PROIECTANT / DESIGNER :		TITLU PROIECT / NAME OF PROJECT :		SPECIFICATIE / POSITION		NUME / NAME		SEMNATURA / SIGNATURE		DATA / DATE		Proiect Tehnic de Executie (PTE)	
						Proiectare și Executie Autostrada Sibiu-Pitești, Sectiunea 2: Boita-Cornetu		Sef Echipa Proiectare / Design Manager		Ing. Battal YILDIZ				06.2026		POD PESTE RAUL VADULUI, DC (STANGA / Left) (Km : 25+181 - 25+271)	
PROIECT CO-FINANTAT DIN FONDUL DE COEZIUNE PRIN PROGRAMUL OPERATIONAL INFRASTRUCTURA MARE						FAZA - 3 : Proiect Tehnic de Executie (PTE) PHASE - 3 : Technical Execution Project		Proiectat / Design		Ing. Emre SENTURK				1/100		POD PESTE RAUL VADULUI, DC (Dreapta / Right) (Km : 25+181 - 25+271)	
						NR. CONTRACT : 92/11066/15.02.2022		Aprobat de / Approved by		Ing. Burak KURTMAN				02.2026		VIA-23 (STANGA / Left) (Km : 25+168.203 - 25+267.117)	
								Verificator Intern / Internal Checker		Ing. M.Kaan BASCUHADAR				Prima Editie / First Issue		VIA-23 (Dreapta / Right) (Km : 25+177.405 - 25+277.103)	
														Nr. / DATA		SECTIUNE TRANSVERSALA CU VEDERE CULEI / CROSS SECTION WITH ABUTMENTS VIEW 1/5	
																SP23YPPSTVIA23TC4002A02	

SECTIUNE TRANSVERSALA CU VEDERE CULEE C2S & C2D /
CROSS SECTION WITH ABUTMENT C2S & C2D VIEW 1:100

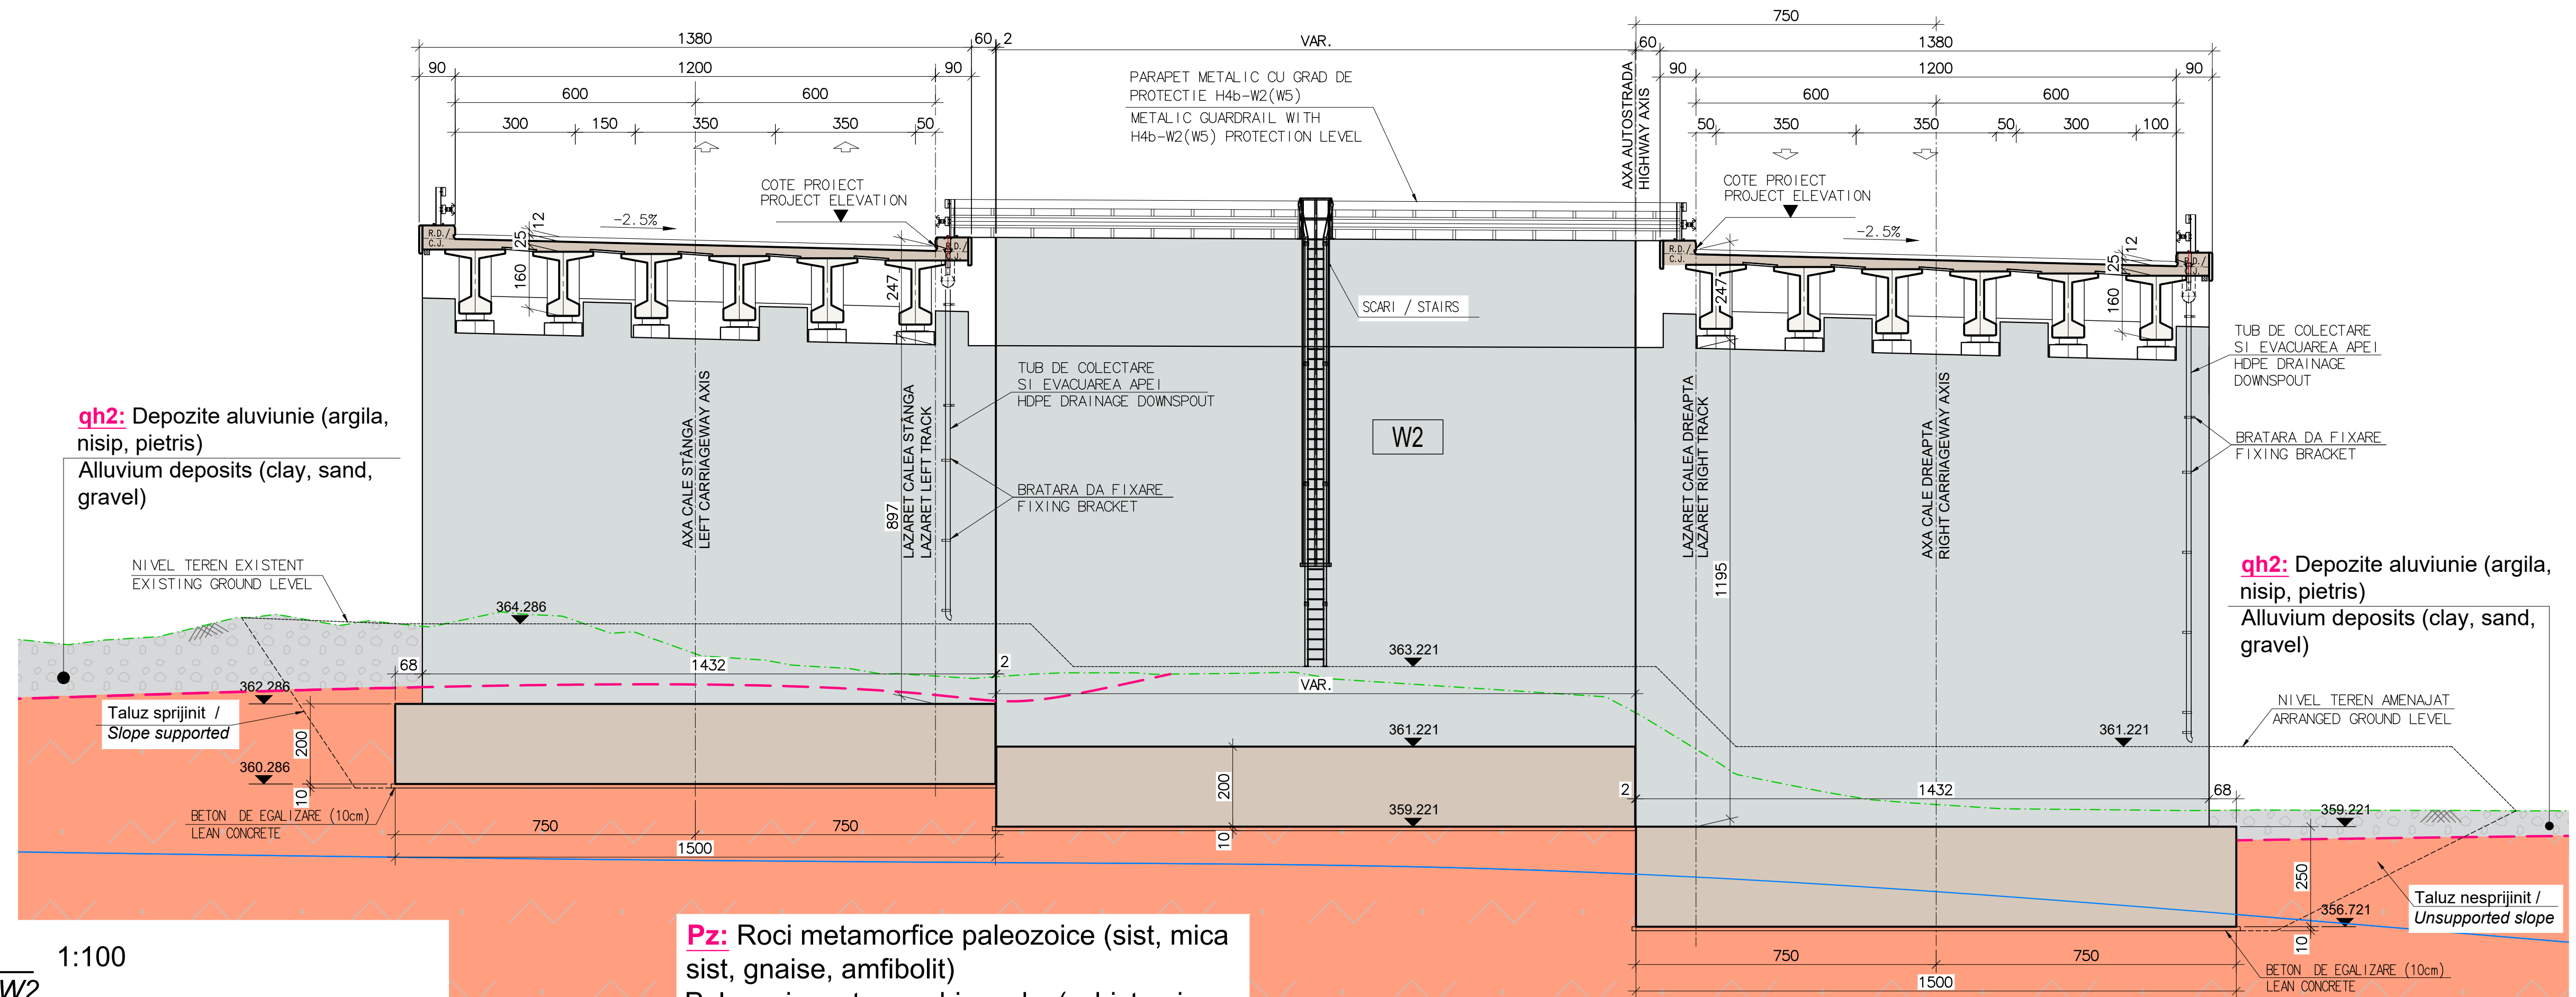

SECTIUNE W2 PERETE DE BETON ARMAT 1:100
SECTION ON REINFORCED CONCRETE WALL W2

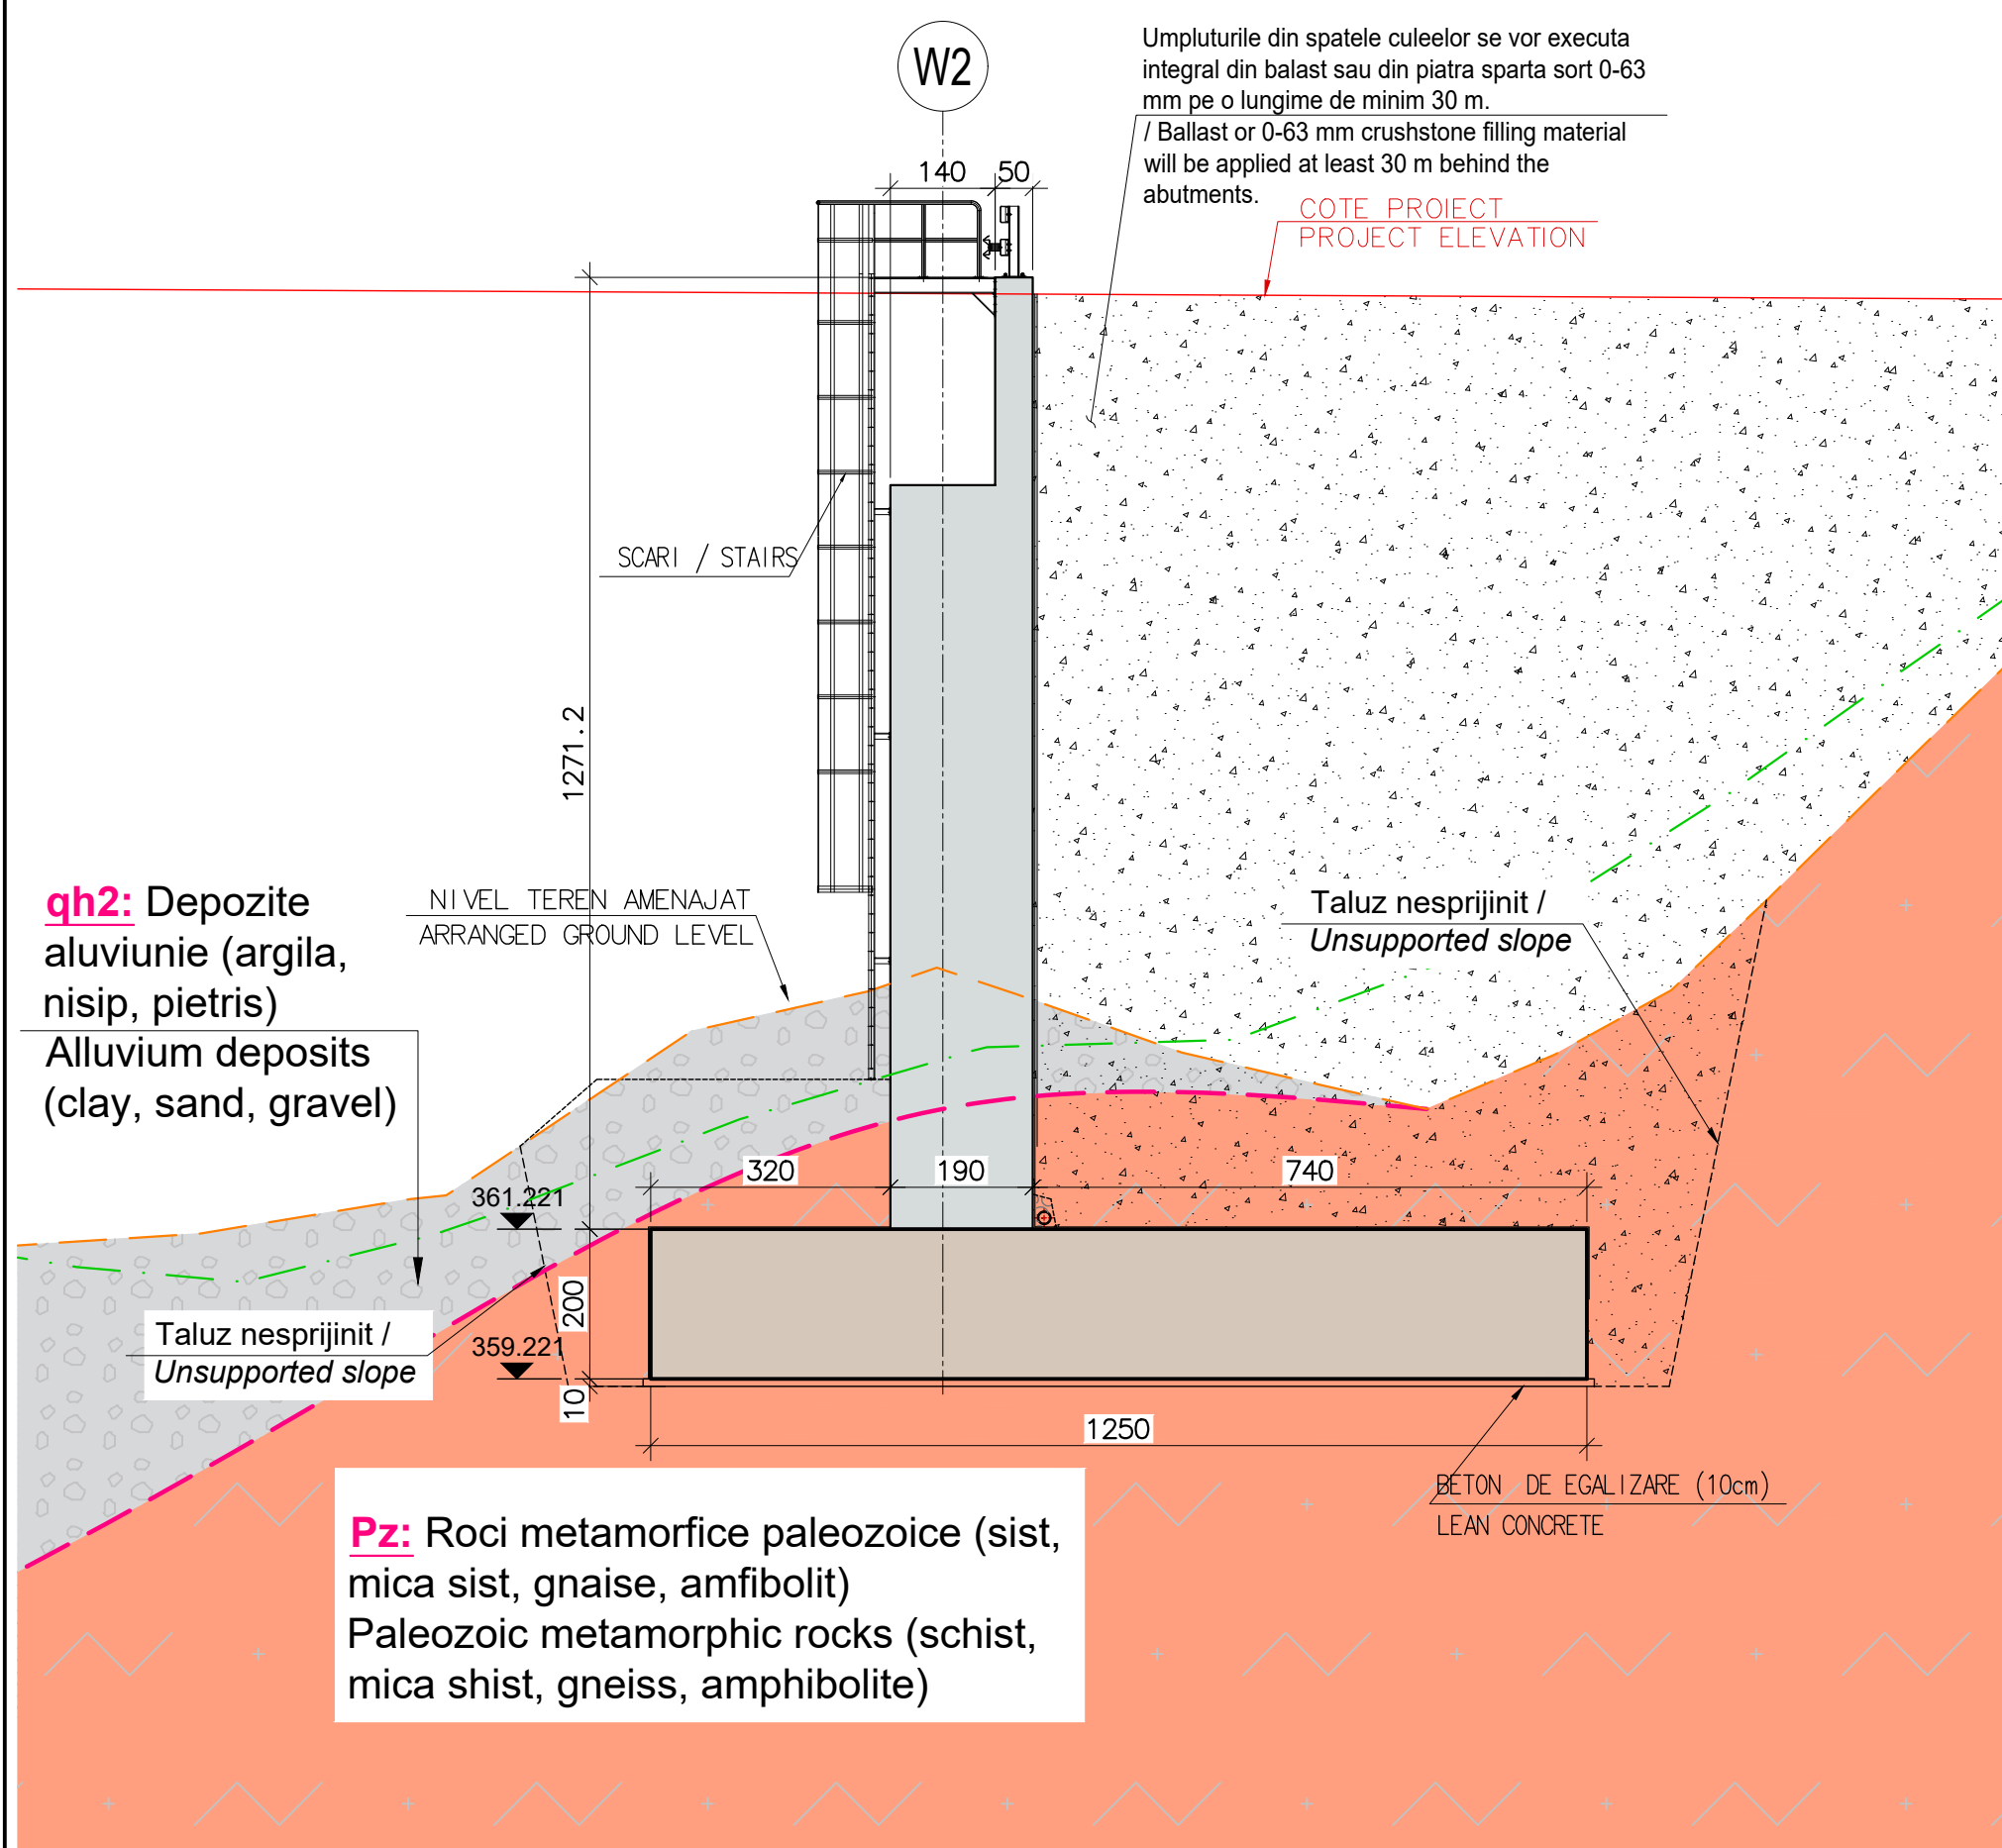

1. Datorita existentei planurilor de sistozitate in masa de roca in zona fundatiilor, dupa excavarea fundatiilor trebuie efectuate verificari cinematice pentru a preveni cedarea datorita discontinuitatilor rocilor.
2. Dupa excavarea fundatiilor, in cazul in care local se intalnesc formatiuni de pamanturi (depozite aluvionare), acestea se vor inlocui cu beton simplu

1. *Because of existence of heavily tectonized schistosity planes in the foundation rock mass, after foundation excavation, kinematical checks must be performed to prevent possible discontinuity controlled failure.*
2. *After foundation excavation if any soil material is encountered locally it will be replaced by plain concrete.*


Pentru sprijinirea debleului necesar construcția podului, vă rugăm să consultați raportul „Lucrări de consolidare – Sector 4 -Breviar de calcul. Km 19+150-44+500, Capitolul 2.3.6 Tabelul 7”.

To support the excavation required for the construction of the bridge, please consult the report "Consolidation Works - Sector 4 - Calculation Brief. Km 19+150-44+500, Chapter 2.3.6 Table 7".

NOTĂ / NOTE :
- TOATE DIMENSIUNILE SUNT DATE IN "cm" DACA NU ESTE SPECIFICAT ALTFEL /
ALL DIMENSIONS ARE IN "cm" UNLESS OTHERWISE SPECIFIED.

[illegible]

SECTIUNE TRANSVERSALA CU VEDERE PILE P1S & P1D /
CROSS SECTION WITH PIER P1S & P1D VIEW 1:100

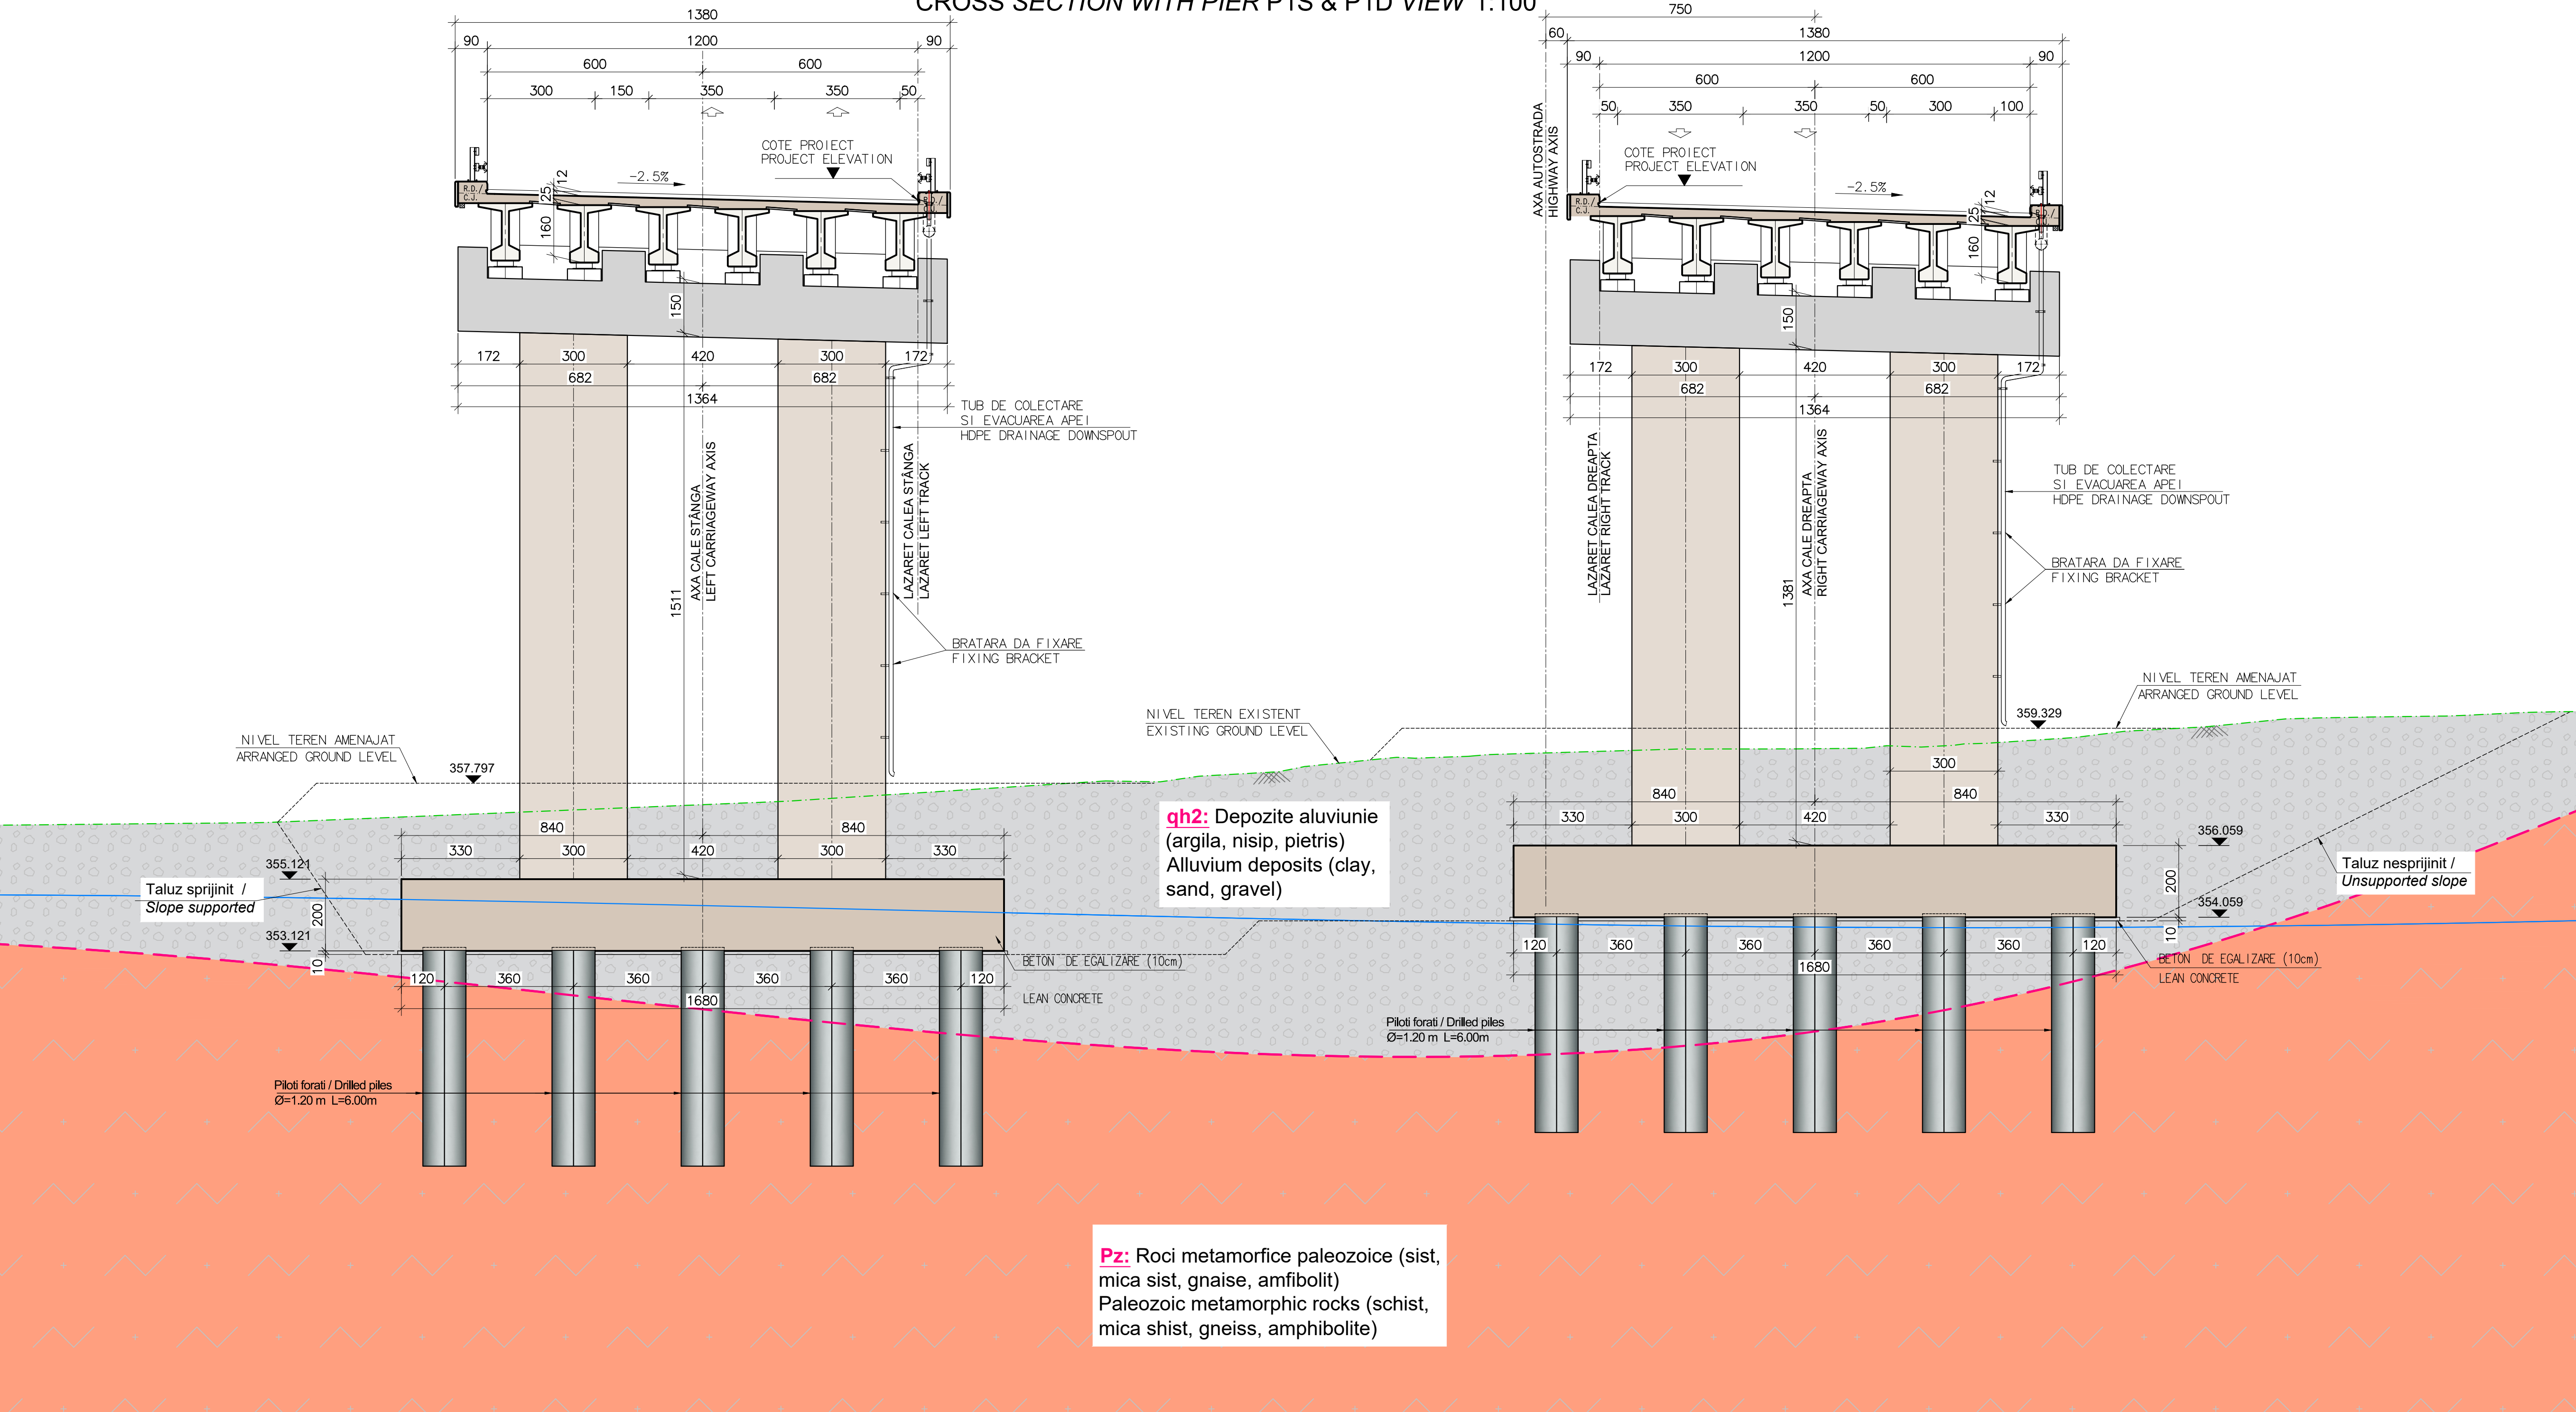

NOTĂ / NOTE :

- Deoarece piloții sunt purtători pe vârf, lungimea încastrării acestora în roca de bază trebuie să fie de minim 1.8 m. (P1S&P1D)
- Since piles are end-bearing piles socketed into bearing rock, socket length has to be satisfied with a minimum 1.8 m depth. (P1S&P1D)

Pentru sprijinirea debleului necesar construcția podului, vă rugăm să consultați raportul „Lucrări de consolidare – Sector 4 -Breviar de calcul. Km 19+150-44+500, Capitolul 2.3.6 Tabelul 7”.


To support the excavation required for the construction of the bridge, please consult the report "Consolidation Works - Sector 4 - Calculation Brief. Km 19+150-44+500, Chapter 2.3.6 Table 7".

NOTĂ / NOTE :
- TOATE DIMENSIUNILE SUNT DATE IN "cm" DACA NU ESTE SPECIFICAT ALTFEL /
ALL DIMENSIONS ARE IN "cm" UNLESS OTHERWISE SPECIFIED.

ORIGINAL SIZE A1

BENEFICIAR / BENEFICIARY :		ANTREPRENOR / CONTRACTOR :		PROIECTANT / DESIGNER :		TITLU PROIECT / NAME OF PROJECT :		SPECIFICATIE POSITION		NUME NAME		SEMNATURA SIGNATURE		DATA / DATE : 06.2026		Proiect Tehnic de Executie (PTE)	
						Proiectare și Executie Autostrada Sibiu-Pitești, Secțiunea 2: Boita-Cornetu		Sef Echipa Proiectare Design Manager		Ing. Battal YILDIZ				SCARA / SCALE : 1/100		POD PESTE RAUL VADULUI, DC (STÂNGA / Left) (Km : 25+181 - 25+271) POD PESTE RAUL VADULUI, DC (Dreapta / Right) (Km : 25+181 - 25+271) VIA-23 (STÂNGA / Left) (Km : 25+168.203 - 25+267.117) VIA-23 (Dreapta / Right) (Km : 25+177.405 - 25+277.103) SECTIUNE TRANSVERSALA CU VEDERE PILE / CROSS SECTION WITH PIERS VIEW 3/5	
PROIECT CO-FINANȚAT DIN FONDUL DE COEZIUNE PRIN PROGRAMUL OPERATIONAL INFRASTRUCTURA MARE						FAZA / PHASE : FAZA - 3 : Proiect Tehnic de Executie (PTE) PHASE - 3 : Technical Execution Project		Aprobat de Approved by Ing. Burak KURTMAN						0 02.2026 Prima Editie / First Issue		SP23YPPSTVIA23TC4004A02	
						NR. CONTRACT : 92/11066/15.02.2022		Verificator Intern Internal Checker Ing. M.Kaan BAŞÇUHADAR						NR. DATA		DESCRIERE / DESCRIPTION	

SECTIONE TRANSVERSALA CU VEDERE PILE P2S & P2D /
CROSS SECTION WITH PIER P2S & P2D VIEW 1:100

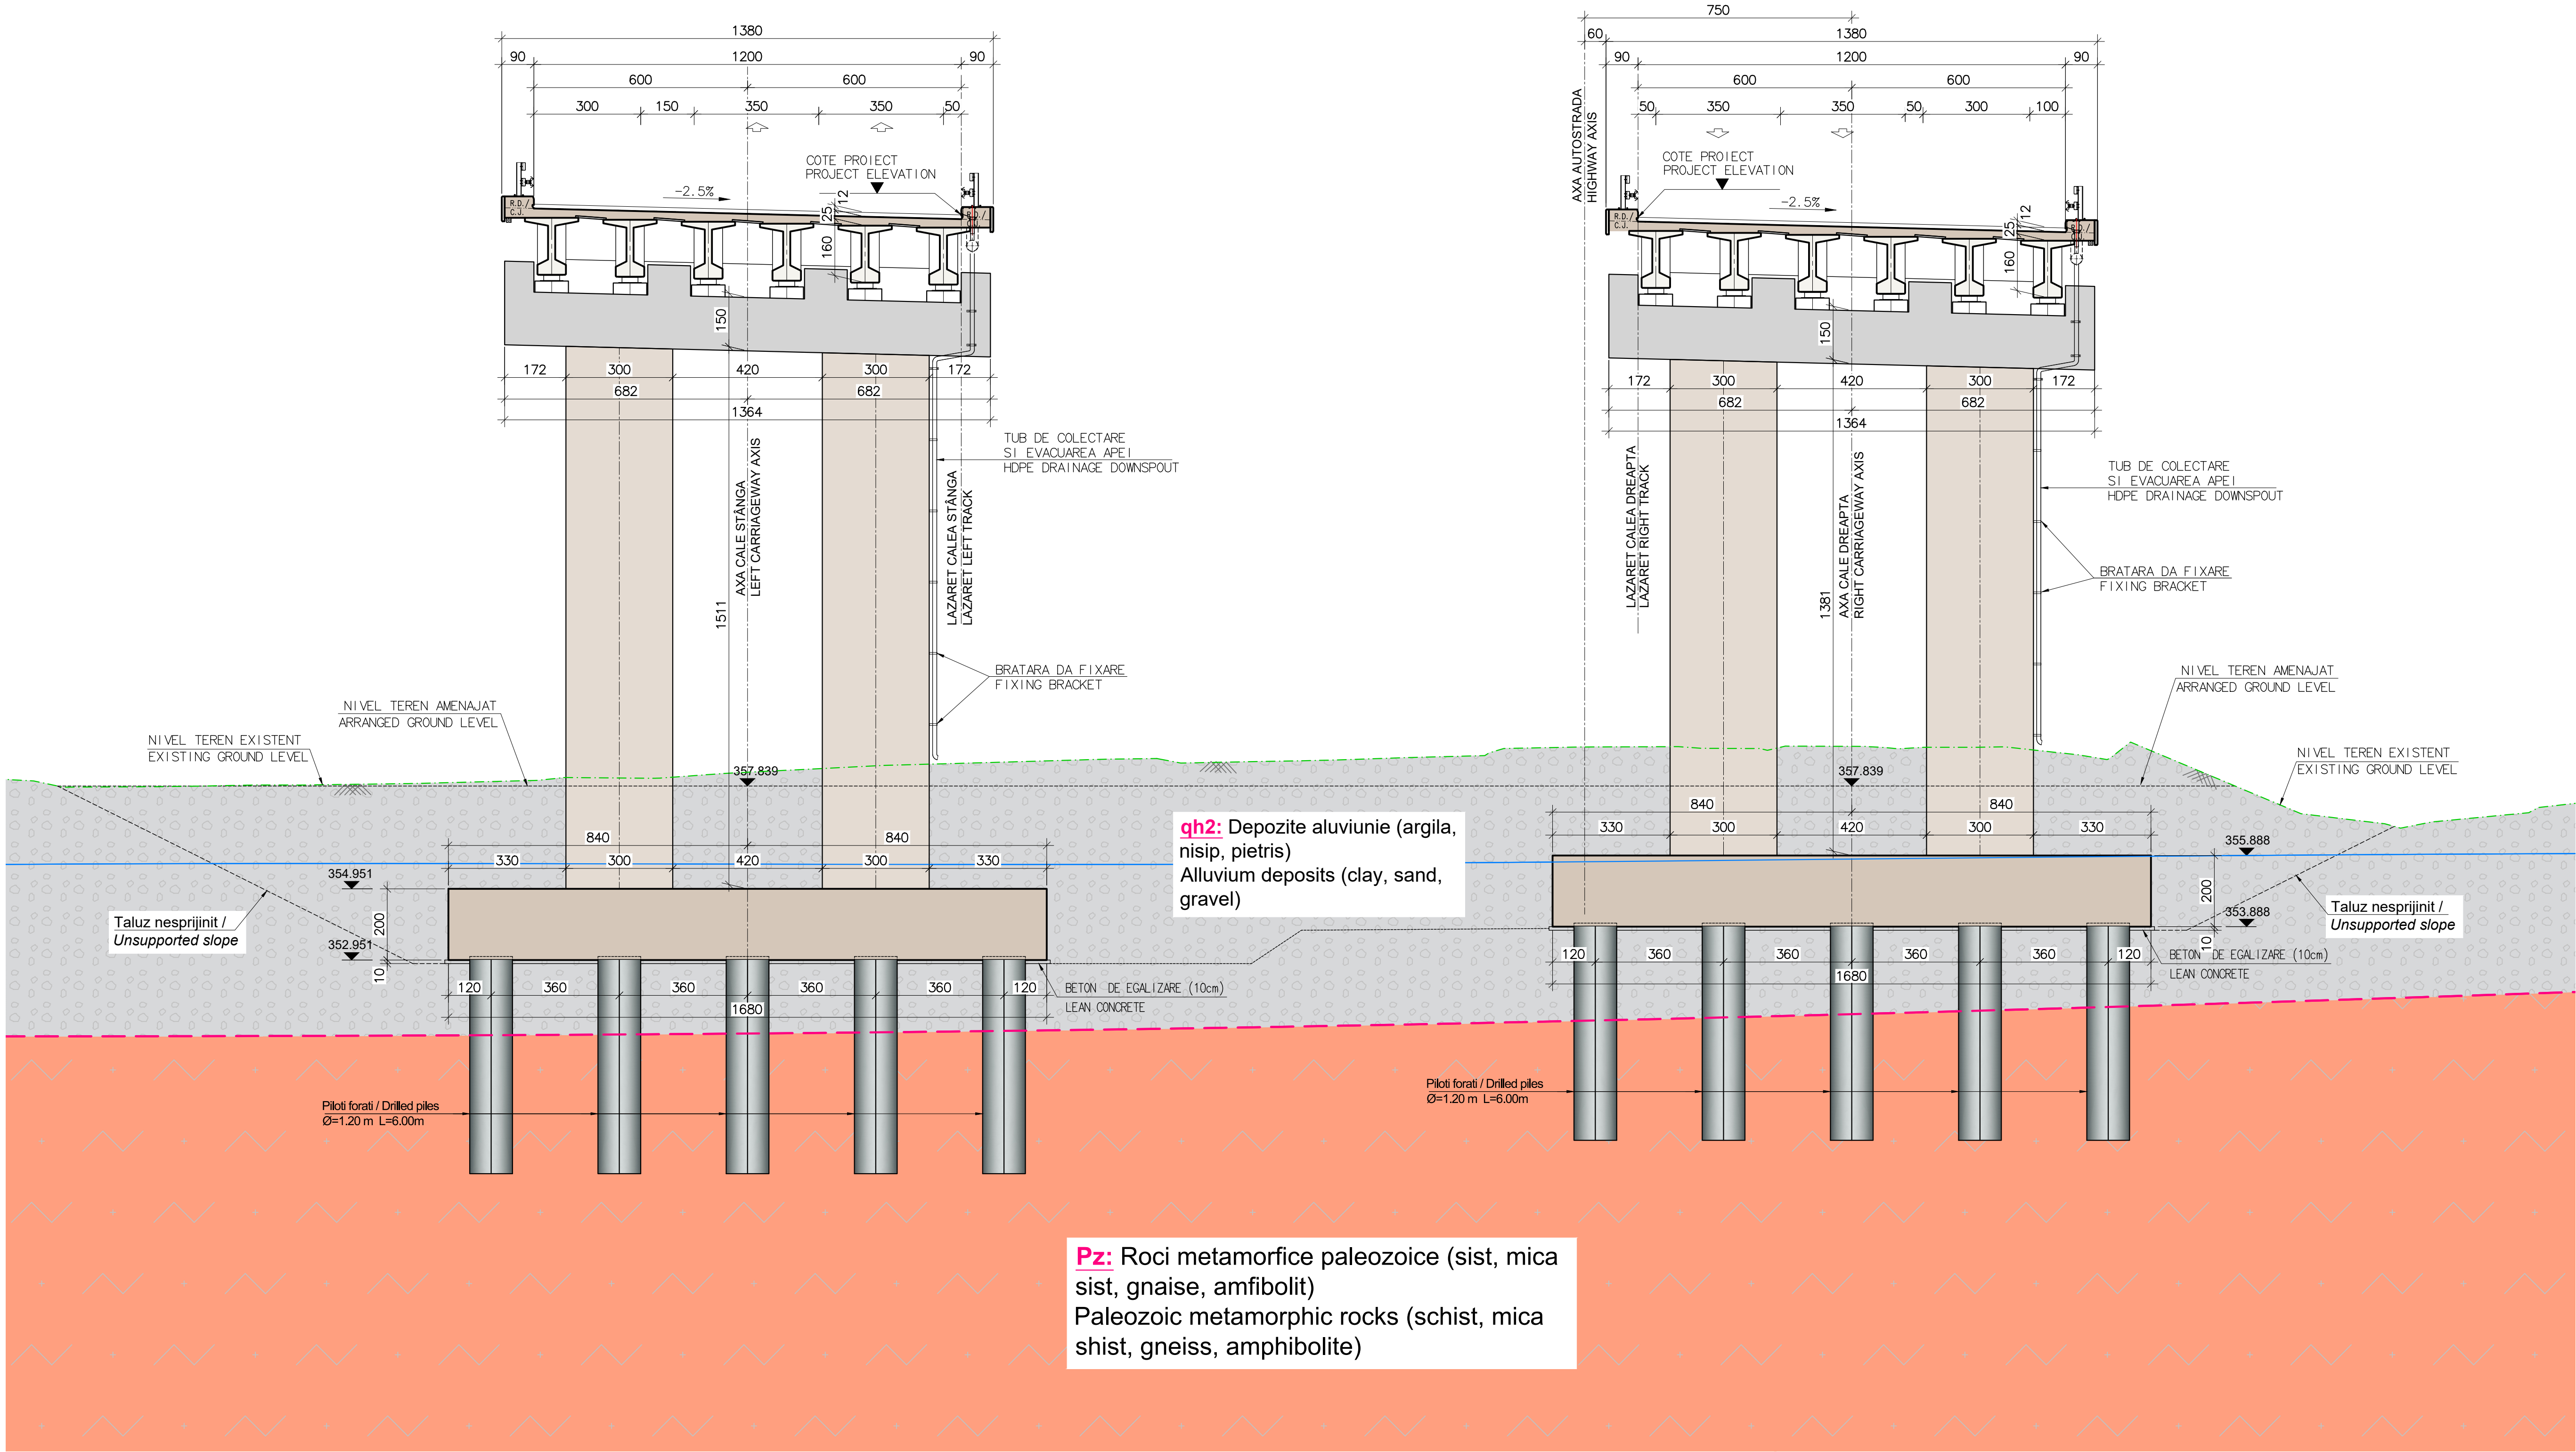

NOTĂ / NOTE :

- Deoarece piloții sunt purtători pe vârf, lungimea încastrării acestora în roca de bază trebuie să fie de minim 1.8 m. (P2S&P2D)
- Since piles are end-bearing piles socketed into bearing rock, socket length has to be satisfied with a minimum 1.8 m depth. (P2S&P2D)

Pentru sprijinirea debleului necesar construcția podului, vă rugăm să consultați raportul „Lucrări de consolidare – Sector 4 -Breviar de calcul. Km 19+150-44+500, Capitolul 2.3.6 Tabelul 7”.

To support the excavation required for the construction of the bridge, please consult the report "Consolidation Works - Sector 4 - Calculation Brief. Km 19+150-44+500, Chapter 2.3.6 Table 7".


NOTĂ / NOTE :

- TOATE DIMENSIUNILE SUNT DATE ÎN "cm" DACA NU ESTE SPECIFICAT ALTTEL / ALL DIMENSIONS ARE IN "cm" UNLESS OTHERWISE SPECIFIED.

ORIGINAL SIZE A1


BENEFICIAR / BENEFICIARY :		ANTREPRENOR / CONTRACTOR :		PROIECTANT / DESIGNER :		TITLU PROIECT / NAME OF PROJECT :		SPECIFICAȚIE POSITION		NUME NAME		SEMNAȚURA SIGNATURE		DATA / DATE :		Proiect Tehnic de Execuție (PTE)	
						Proiectare și Execuție Autostradă Sibiu-Pitești, Secțiunea 2: Boita-Cornetu		Sef Echipa Proiectare Design Manager		Ing. Battal YILDIZ				06.2026		POD PESTE RAUL VADULUI, DC (STÂNGA / Left) (Km : 25+181 - 25+271)	
PROIECT CO-FINANȚAT DIN FONDUL DE COEZIUNE PRIN PROGRAMUL OPERATIONAL INFRASTRUCTURA MARE						FAZA - 3 : Proiect Tehnic de Execuție (PTE)		Proiectat Design		Ing. Emre ŞENTÜRK				1/100		POD PESTE RAUL VADULUI, DC (Dreapta / Right) (Km : 25+181 - 25+271)	
						NR. CONTRACT : 92/11066/15.02.2022		Aprobat de Approved by		Ing. Burak KURTMAN				02.2026		VIA-23 (STÂNGA / Left) (Km : 25+168.203 - 25+267.117)	
								Verificator Intern Internal Checker		Ing. M.Kaan BAŞÇUHADAR				02.2026		VIA-23 (Dreapta / Right) (Km : 25+177.405 - 25+277.103)	
																SECTIUNE TRANSVERSALA CU VEDERE PILE / CROSS SECTION WITH PIERS VIEW 4/5	
																SP23YPPSTVIA23TC4005A02	

1:100

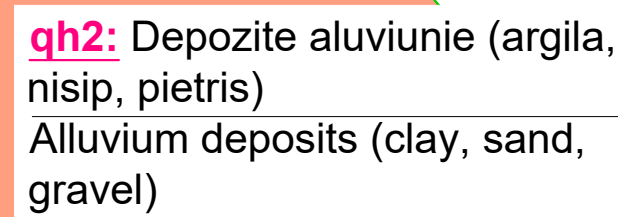


Pz: Roci metamorifice paleozoice (sist, mica sist, gnaise, amfibolit)
Paleozoic metamorphic rocks (schist, mica schist, gneiss, amphibolite)

1:100

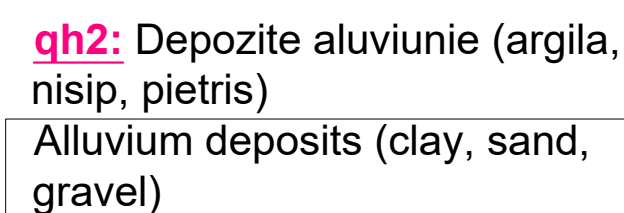

Pz: Roci metamorifice paleozoice (sist, mica sist, gnaise, amfibolit)
Paleozoic metamorphic rocks (schist, mica schist, gneiss, amphibolite)

1:100

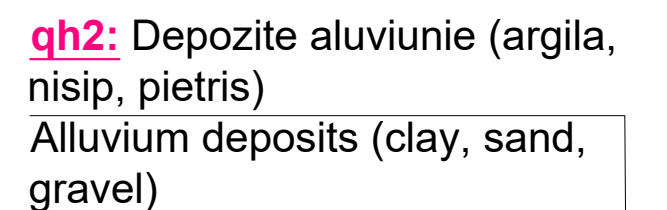

Pz: Roci metamorfice paleozoice (sist, mica sist, gnaise, amfibolit)
Paleozoic metamorphic rocks (schist, mica schist, gneiss, amphibolite)

1. Datorita existentei planurilor de sistozitate in masa de roca in zona fundatiilor, dupa excavarea fundatiilor trebuie efectuate verificari cinematice pentru a preveni cedarea datorita discontinuitatilor rocilor.
 2. Dupa excavarea fundatiilor, in cazul in care local se intalnesc formatiuni de pamanturi (depozite aluvionare), acestea se vor inlocui cu beton simplu
-
1. *Because of existence of heavily tectonized schistosity planes in the foundation rock mass, after foundation excavation, kinematical checks must be performed to prevent possible discontinuity controlled failure.*
 2. *After foundation excavation if any soil material is encountered locally it will be replaced by plain concrete.*

Pentru sprijinirea debleului necesar construcția podului, vă rugăm să consultați raportul „Lucrări de consolidare – Sector 4 -Breviar de calcul. Km 19+150-44+500, Capitolul 2.3.6 Tabelul 7”.

To support the excavation required for the construction of the bridge, please consult the report "Consolidation Works - Sector 4 - Calculation Brief. Km 19+150-44+500, Chapter 2.3.6 Table 7".

NOTĂ / NOTE :
- TOATE DIMENSIUNILE SUNT DATE IN "cm" DACA NU ESTE SPECIFICAT ALTFEL /
ALL DIMENSIONS ARE IN "cm" UNLESS OTHERWISE SPECIFIED.

BENEFICIAR / BENEFICIARY :				ANTREPRENOR / CONTRACTOR :				PROIECTANT / DESIGNER :				TITLU PROIECT / NAME OF PROJECT :				SPECIFICAȚIE / POSITION				NUME / NAME				SEMNAȚURA / SIGNATURE				REVIZITĂ / REVISIONS				DATA / DATE :				Proiect Tehnic de Executie (PTE)							
UNIUNEA EUROPEANĂ GUVERNUL ROMÂNIEI MINISTERUL TRANSPORTURILOR CNAI-R PROIECT CO-FINANȚAT DIN FONDUL DE COEZIUNE PRIN PROGRAMUL OPERAȚIONAL INFRASTRUCTURĂ MARE				YOKSEL PROJE								Proiectare și Executare Autostrada Sibiu-Pitești, Secțiunea 2: Boita-Cornetu				FAZA / PHASE :				NR. CONTRACT :				ing. Battali YILDIZ								2 06.2026				1/100				POD PESTE RAUL VADULUI, DC (STÂNGA / Left) (Km : 25+181 - 25+271) POD PESTE RAUL VADULUI, DC (Dreapta / Right) (Km : 25+181 - 25+271) VIA-23 (STÂNGA / Left) (Km : 25+168.205 - 25+267.117) VIA-23 (Dreapta / Right) (Km : 25+177.405 - 25+277.103) SECȚIUNE TRANSVERSALA CU VEDERE PERETE DE RETINERE / CROSS SECTION WITH RETAINING WALL VIEW 5/5			
																ing. Emre ŞENTÜRK												1 04.2026															
																ing. Burak KURTMAN												0 02.2026															
																ing. M. Kaan BAŞÇUHADAR																											
																				DESCRIERE / DESCRIPTION :																							
																92/11066/15.02.2022				92/11066/15.02.2022																				SP23YPSPSTVIA423TC40005A02			